


01

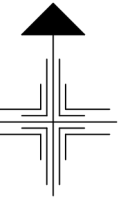

NOTES:

1. DIMENSIONS TO BE CHECKED AS PER SITE CONDITION.
2. ALL DIMENSIONS ARE IN FT AND INCHES UNLESS MENTIONED
3. DRAWINGS ARE TO BE READ AND NOT TO BE SCALED
4. ARCHITECT MUST BE NOTIFIED IF ANY DISCREPANCY OCCURS BETWEEN THE DRAWING AND THE SITE BEFORE STARTING THE WORK

DRAWN: POTLURI CHINMAYI

ROLL NO: 22WU0301110

PROGRAM: INTERIOR DESIGN SEM-V


DATE: 20-08-2024

SCALE: N.T.S.


SHEET TITLE: SITE PLAN

PROJECT TITLE: 2BHK VILLA

SIGNATURE

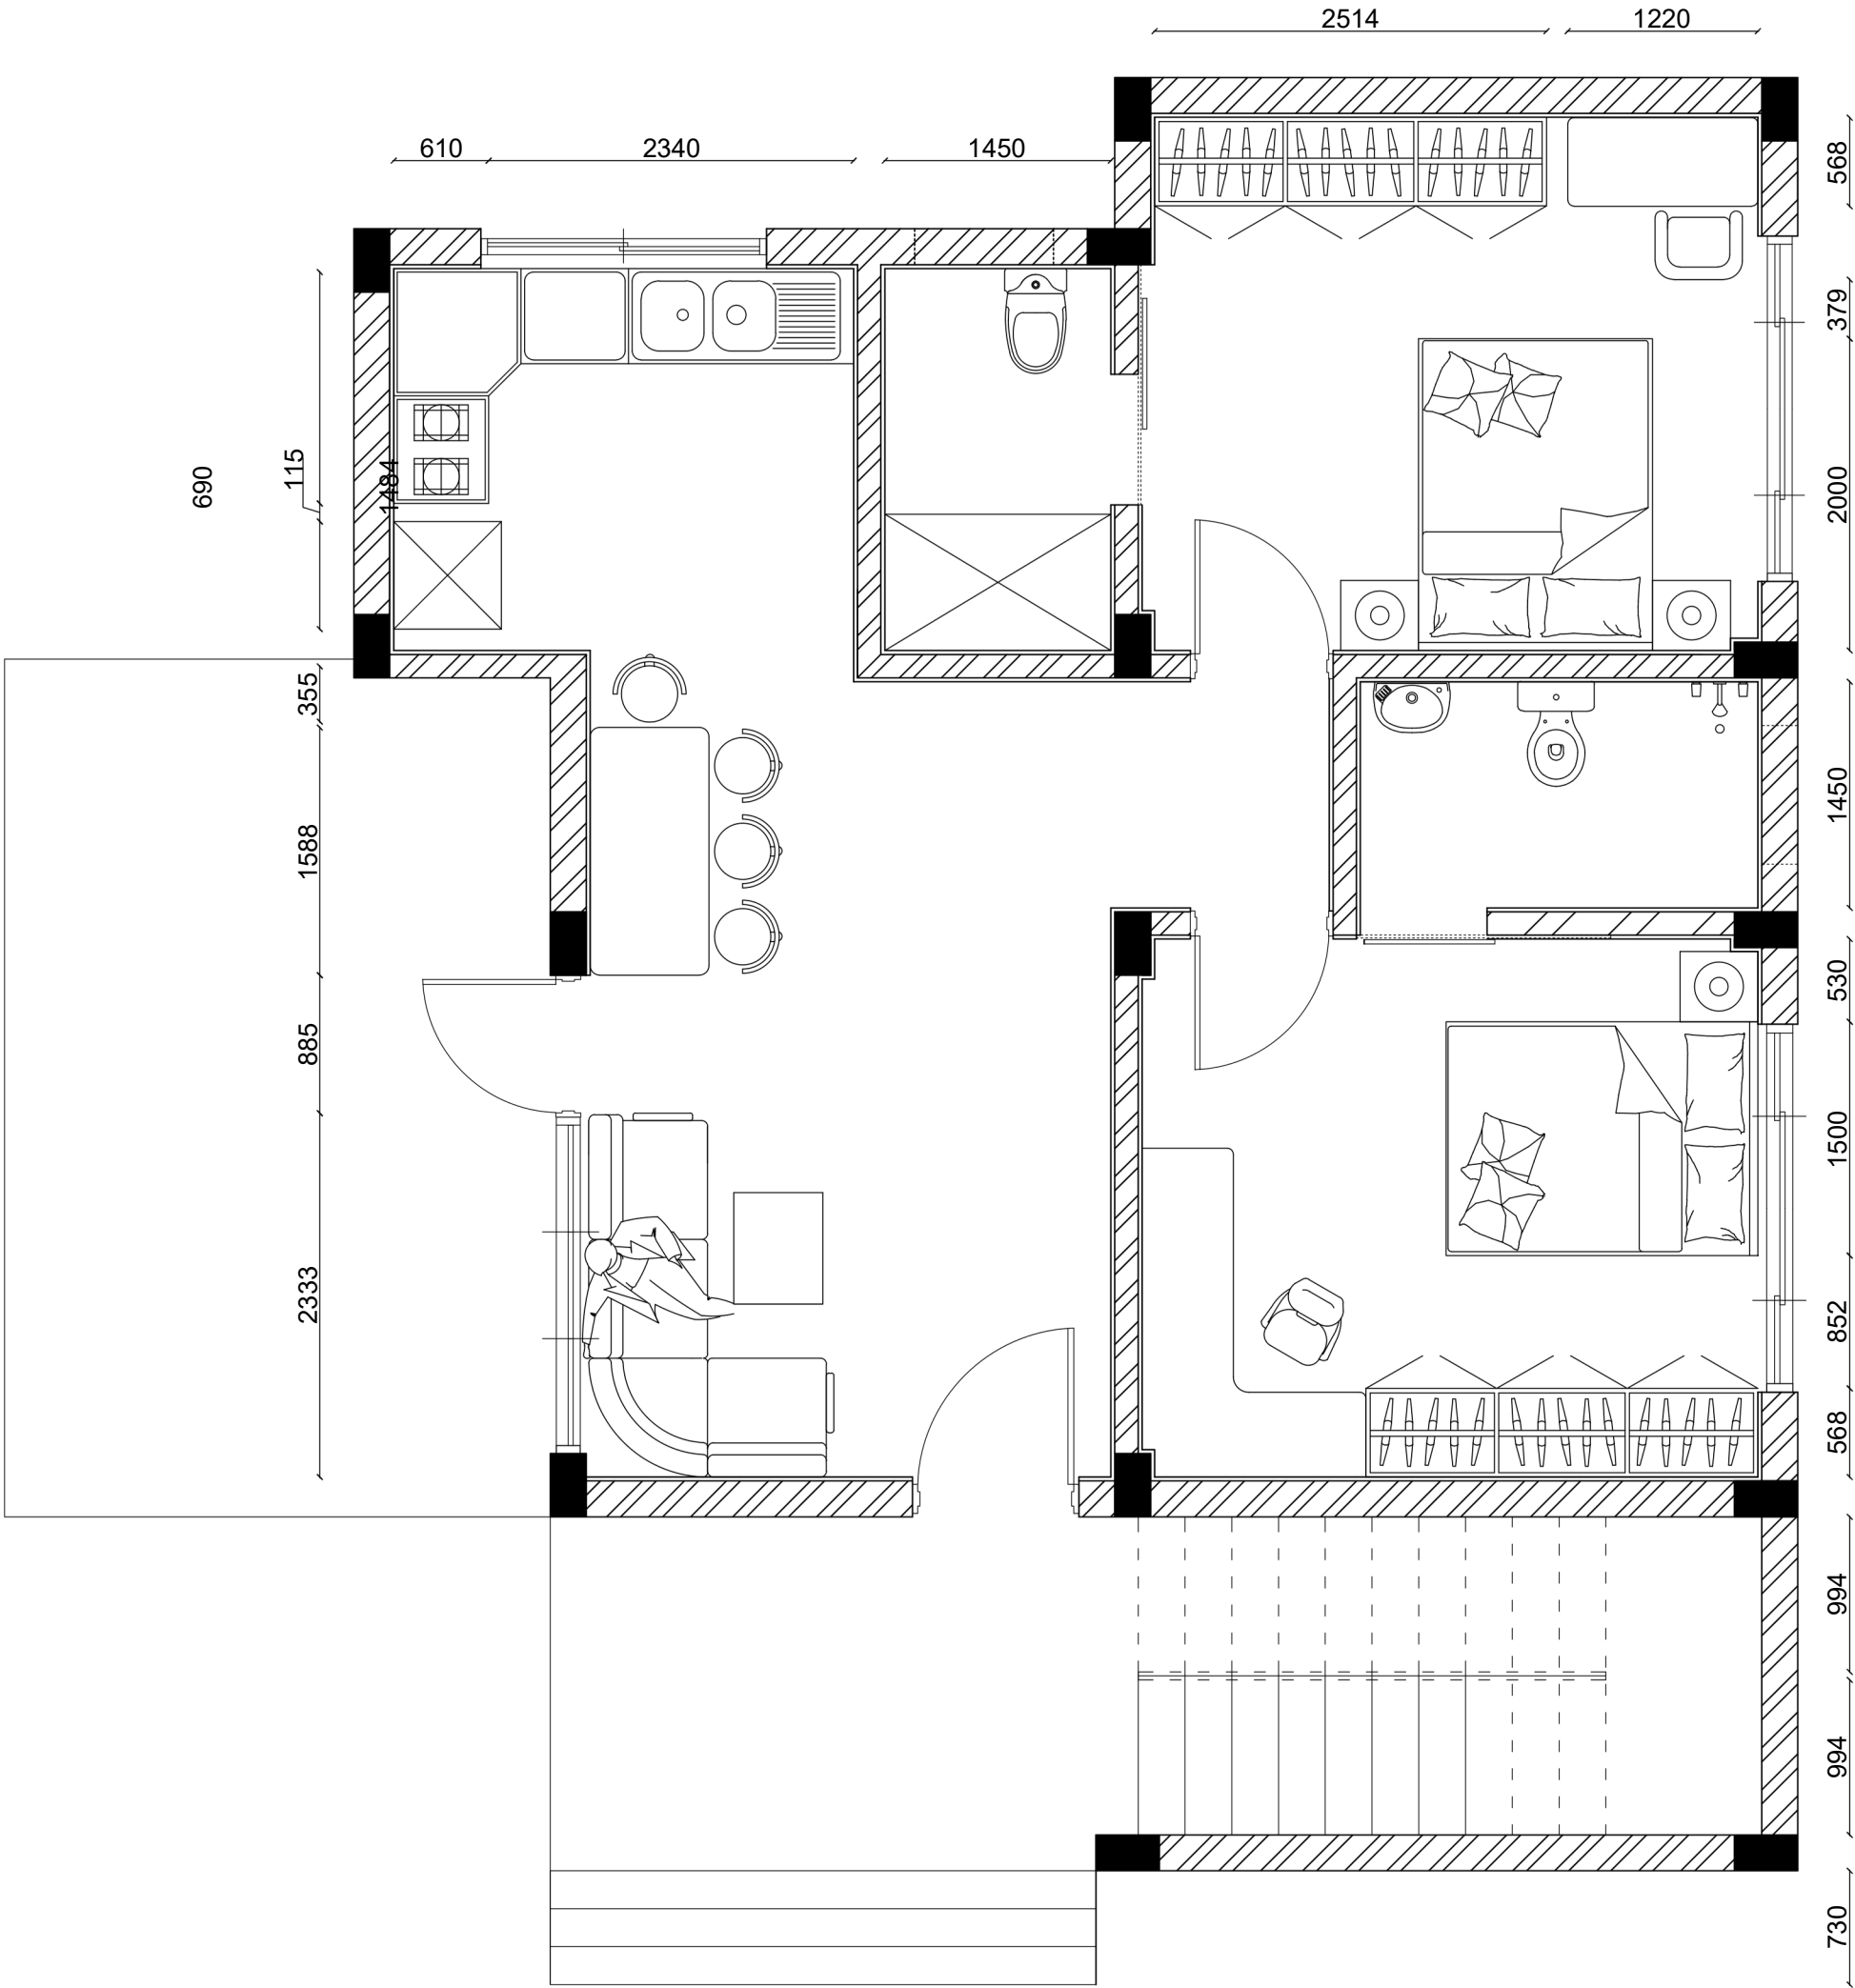

02














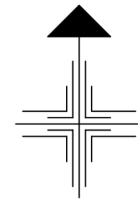



NOTES:

1. DIMENSIONS TO BE CHECKED AS PER SITE CONDITION.
2. ALL DIMENSIONS ARE IN FT AND INCHES UNLESS MENTIONED
3. DRAWINGS ARE TO BE READ AND NOT TO BE SCALED
4. ARCHITECT MUST BE NOTIFIED IF ANY DISCREPANCY OCCURS BETWEEN THE DRAWING AND THE SITE BEFORE STARTING THE WORK


DRAWN:	POTLURI CHINMAYI
ROLL NO:	22WU0301110
PROGRAM:	INTERIOR DESIGN SEM-V
DATE:	20-08-2024
SCALE:	N.T.S.
SHEET TITLE:	SCHEMATIC PLAN
PROJECT TITLE:	2BHK VILLA

SIGNATURE

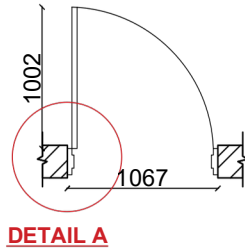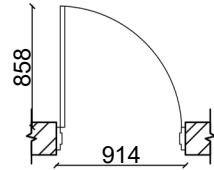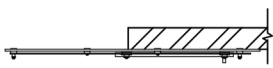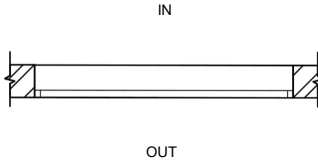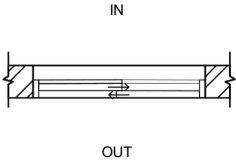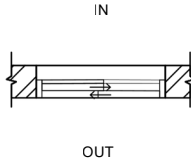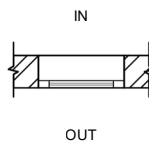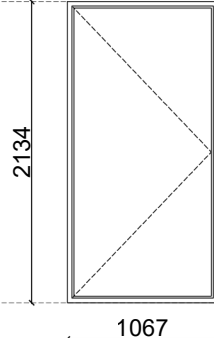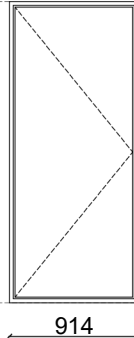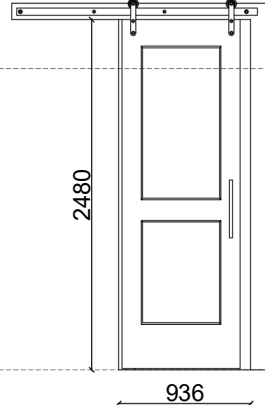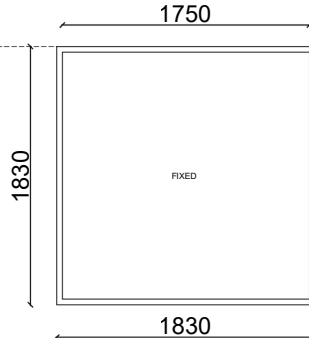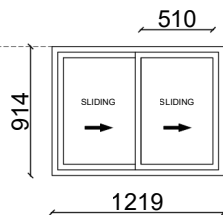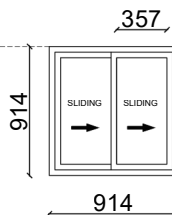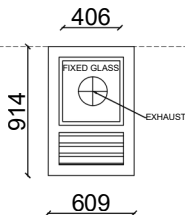ITEM TYPE	D1 - (1067 X 1002mm) DOOR	D1 - (914 X 914mm) DOOR	D2 - (609 X 914mm) SLIDING DOOR WITH FIXED WINDOWS	W1 - (1830 X 1830mm) FIXED WINDOW	W2 - (914 X 2134mm) SLIDING WINDOW	W2 - (914 X 914mm) SLIDING WINDOW	V1 - (609 X 914mm) VENTILATOR
QTY	2	1	1	3	3	1	1
PLAN							
ELEVATION							
LINTEL LVL - 1							
FINISHED FLOOR LVL							
							
REF IMAGE							

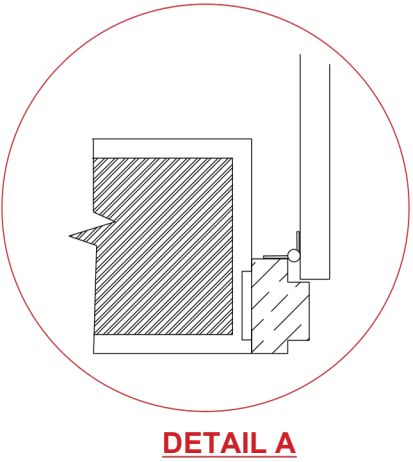

03

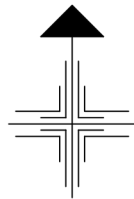

NOTES:

- DIMENSIONS TO BE CHECKED AS PER SITE CONDITION.
- ALL DIMENSIONS ARE IN FT AND INCHES UNLESS MENTIONED
- DRAWINGS ARE TO BE READ AND NOT TO BE SCALED
- ARCHITECT MUST BE NOTIFIED IF ANY DISCREPANCY OCCURS BETWEEN THE DRAWING AND THE SITE BEFORE STARTING THE WORK

DRAWN: POTLURI CHINMAYI

ROLL NO: 22WU0301110


PROGRAM: INTERIOR DESIGN SEM-V

DATE: 20-08-2024

SCALE: N.T.S.

SHEET TITLE: DOOR AND WINDOW SCHEDULE

PROJECT TITLE: 2BHK VILLA

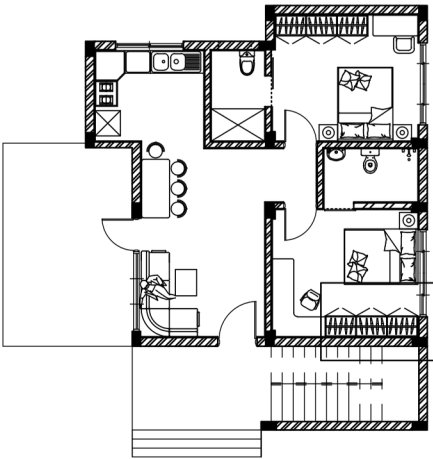

KEY PLAN



NOTES:

1. DIMENSIONS TO BE CHECKED AS PER SITE CONDITION.
2. ALL DIMENSIONS ARE IN FT AND INCHES UNLESS MENTIONED
3. DRAWINGS ARE TO BE READ AND NOT TO BE SCALED
4. ARCHITECT MUST BE NOTIFIED IF ANY DISCREPANCY OCCURS BETWEEN THE DRAWING AND THE SITE BEFORE STARTING THE WORK

DRAWN: POTLURI CHINMAYI

ROLL NO: 22WU0301110


PROGRAM: INTERIOR DESIGN
SEM-V

DATE: 20-08-2024


SCALE: N.T.S.

SHEET TITLE: KITCHEN DETAILS


PROJECT TITLE: 2BHK VILLA

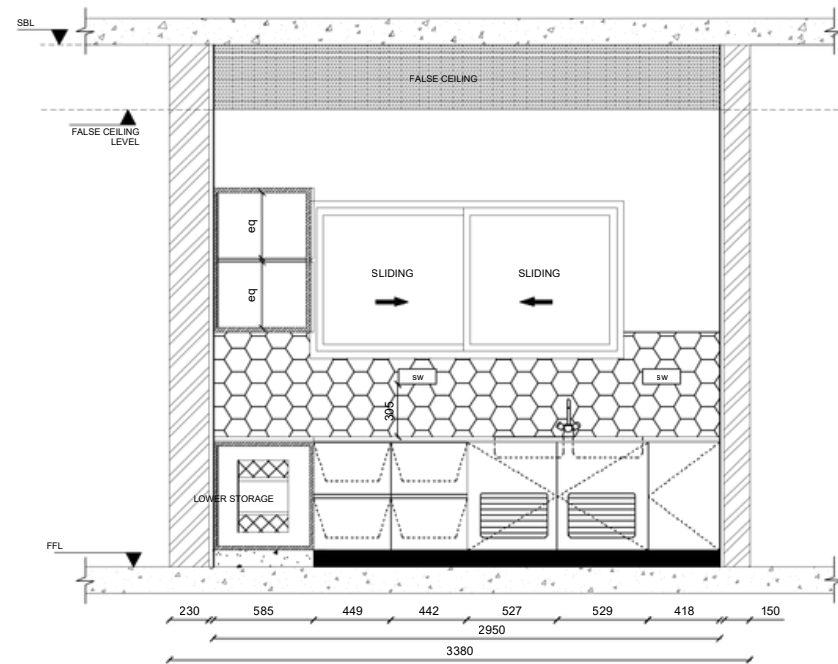


SECTION AA'

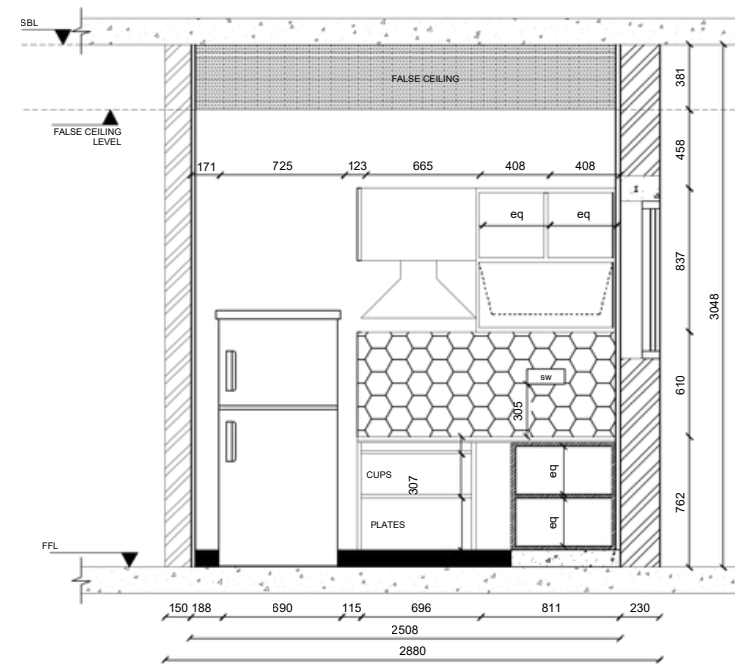


SECTION BB'

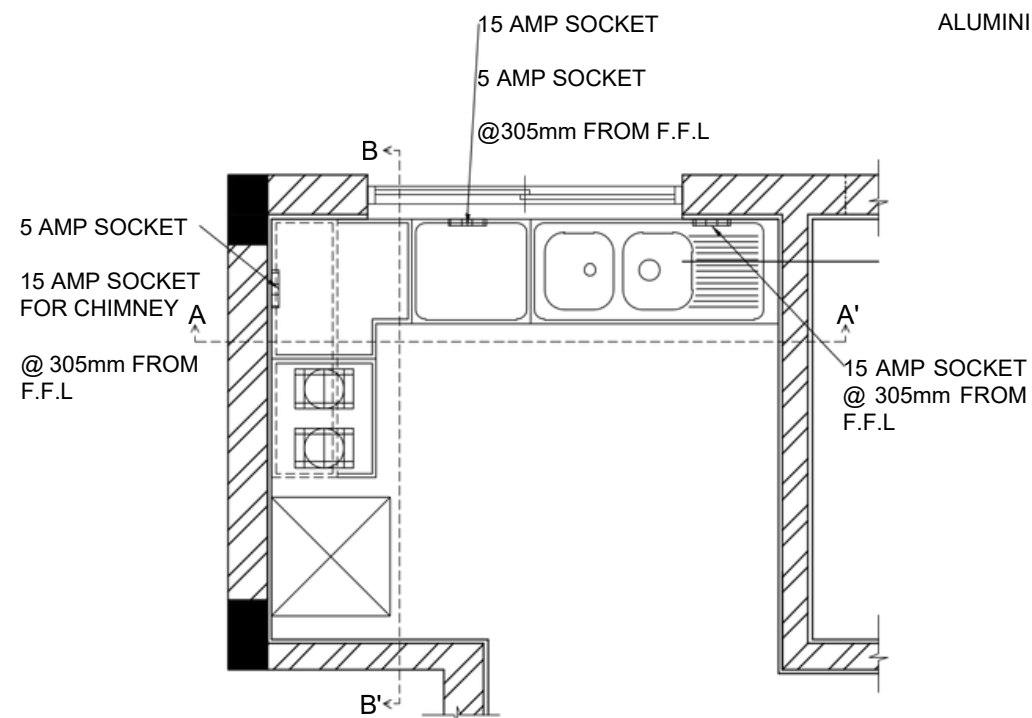


PLAN

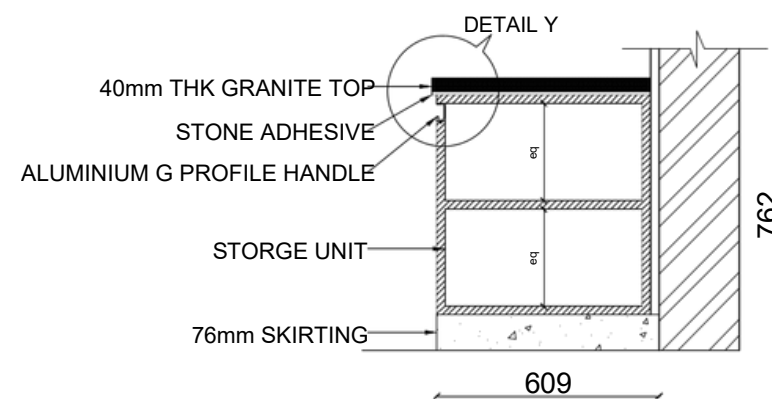


DETAIL X

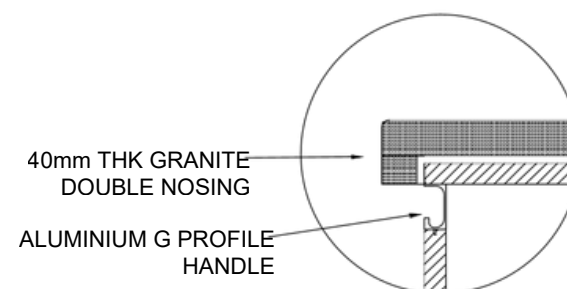

DETAIL Y

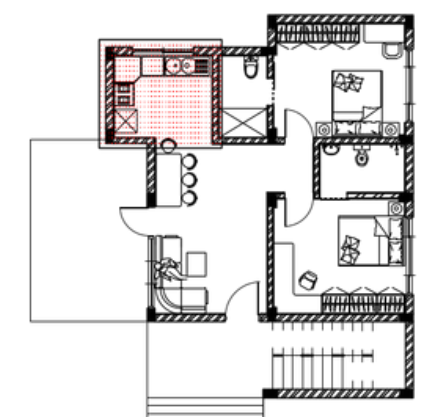


KEY PLAN

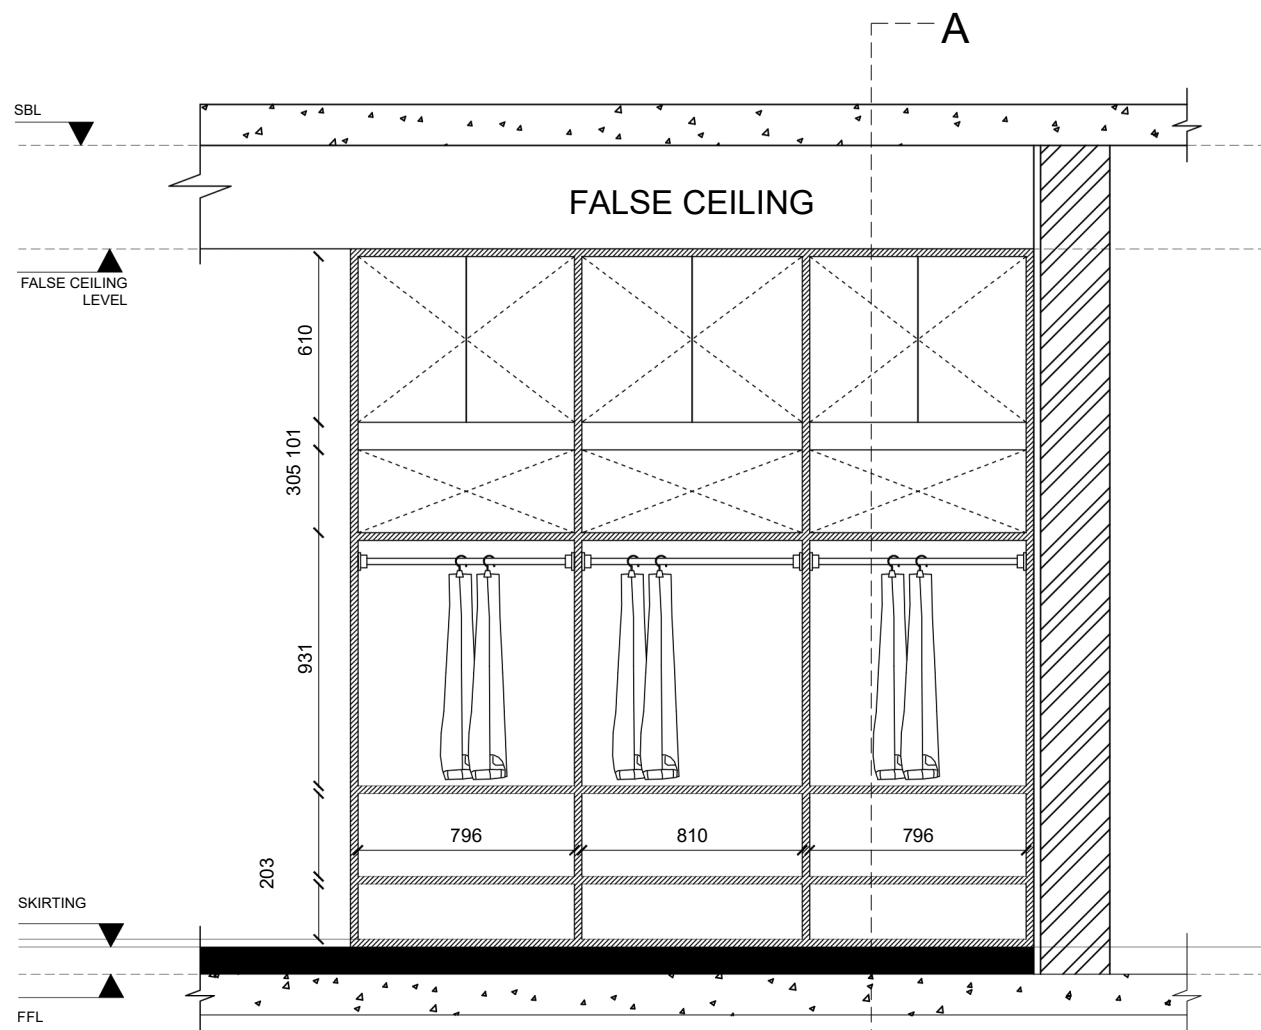


SECTIONAL ELEVATION


A'

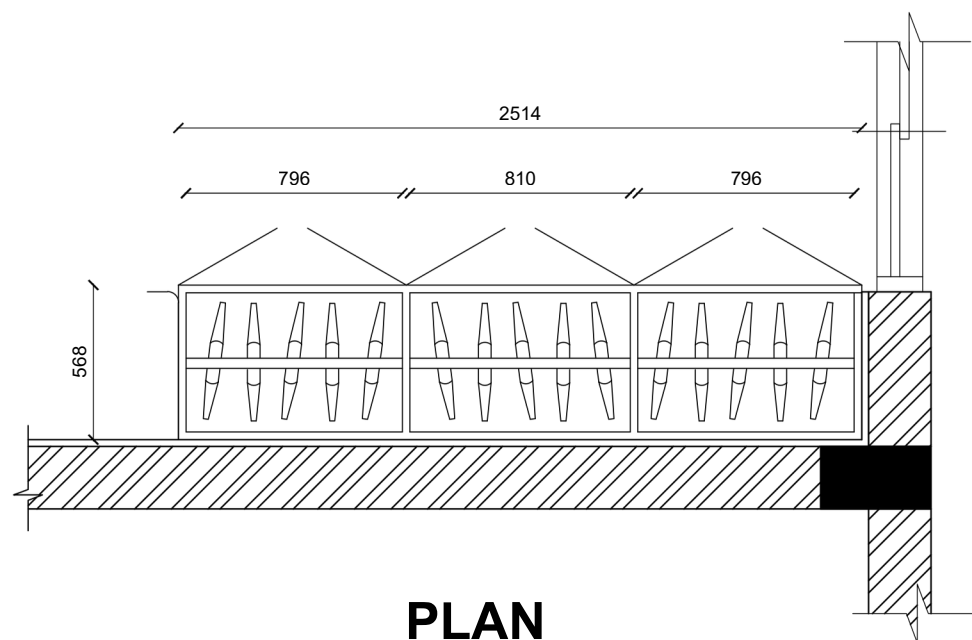


PLAN

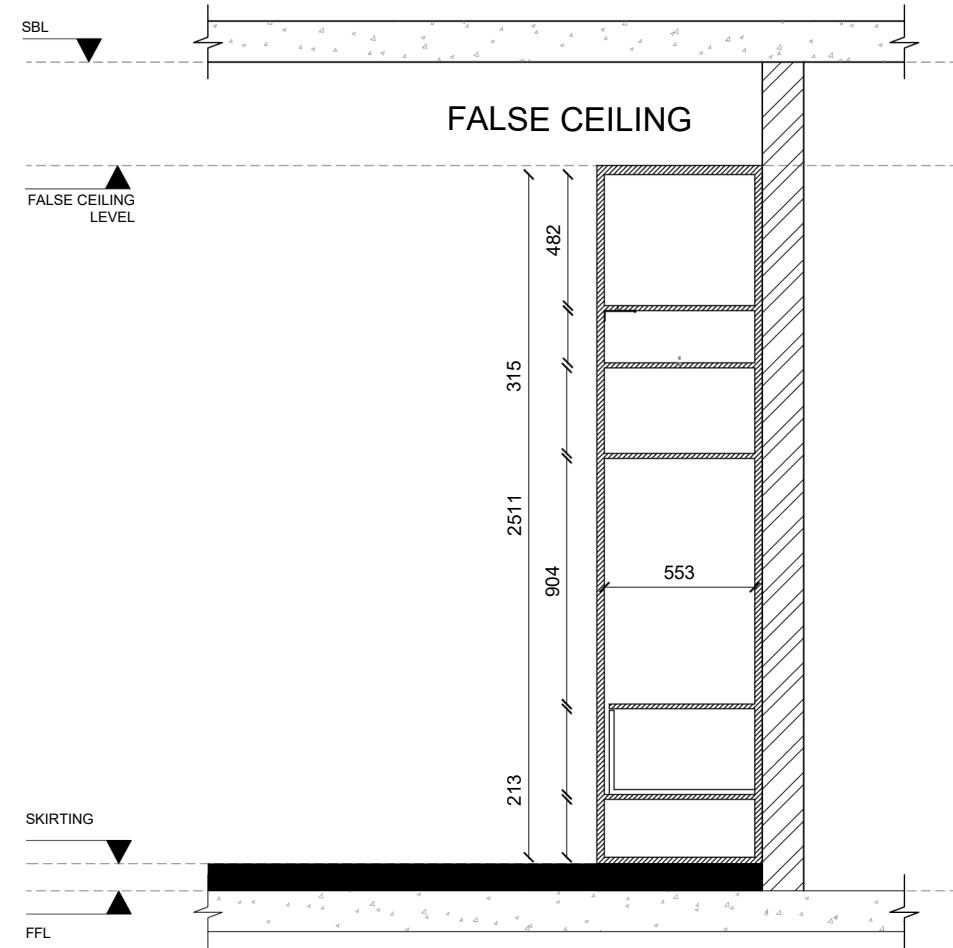

SECTION AA'

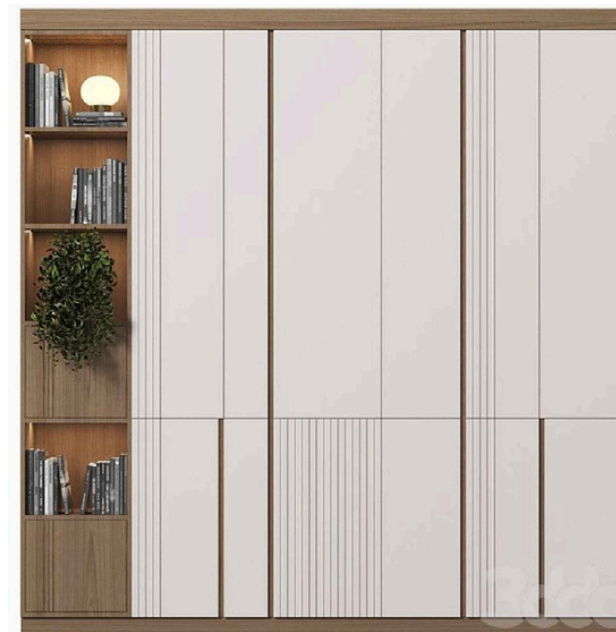

05

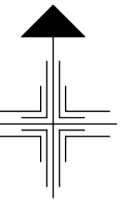

NOTES:

1. DIMENSIONS TO BE CHECKED AS PER SITE CONDITION.
2. ALL DIMENSIONS ARE IN FT AND INCHES UNLESS MENTIONED
3. DRAWINGS ARE TO BE READ AND NOT TO BE SCALED
4. ARCHITECT MUST BE NOTIFIED IF ANY DISCREPANCY OCCURS BETWEEN THE DRAWING AND THE SITE BEFORE STARTING THE WORK

DRAWN: POTLURI CHINMAYI

ROLL NO: 22WU0301110


PROGRAM: INTERIOR DESIGN SEM-V

DATE: 20-08-2024

SCALE: N.T.S.


SHEET TITLE: WARDROBE DETAILS

PROJECT TITLE: 2BHK VILLA

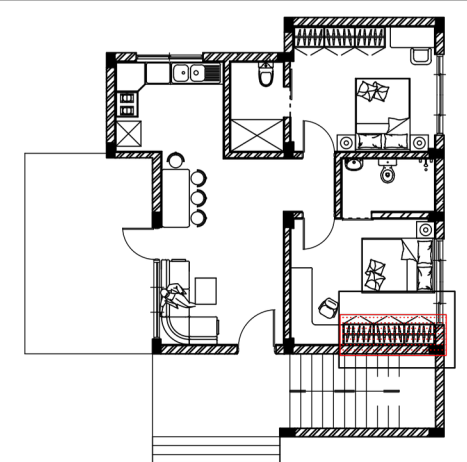

KEY PLAN

06

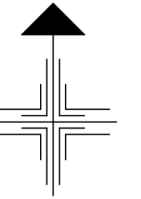

NOTES:

1. DIMENSIONS TO BE CHECKED AS PER SITE CONDITION.
2. ALL DIMENSIONS ARE IN FT AND INCHES UNLESS MENTIONED
3. DRAWINGS ARE TO BE READ AND NOT TO BE SCALED
4. ARCHITECT MUST BE NOTIFIED IF ANY DISCREPANCY OCCURS BETWEEN THE DRAWING AND THE SITE BEFORE STARTING THE WORK

DRAWN: POTLURI CHINMAYI

ROLL NO: 22WU0301110


PROGRAM: INTERIOR DESIGN SEM-V

DATE: 20-08-2024


SCALE: N.T.S.

SHEET TITLE: WARDROBE DETAILS


PROJECT TITLE: 2BHK VILLA

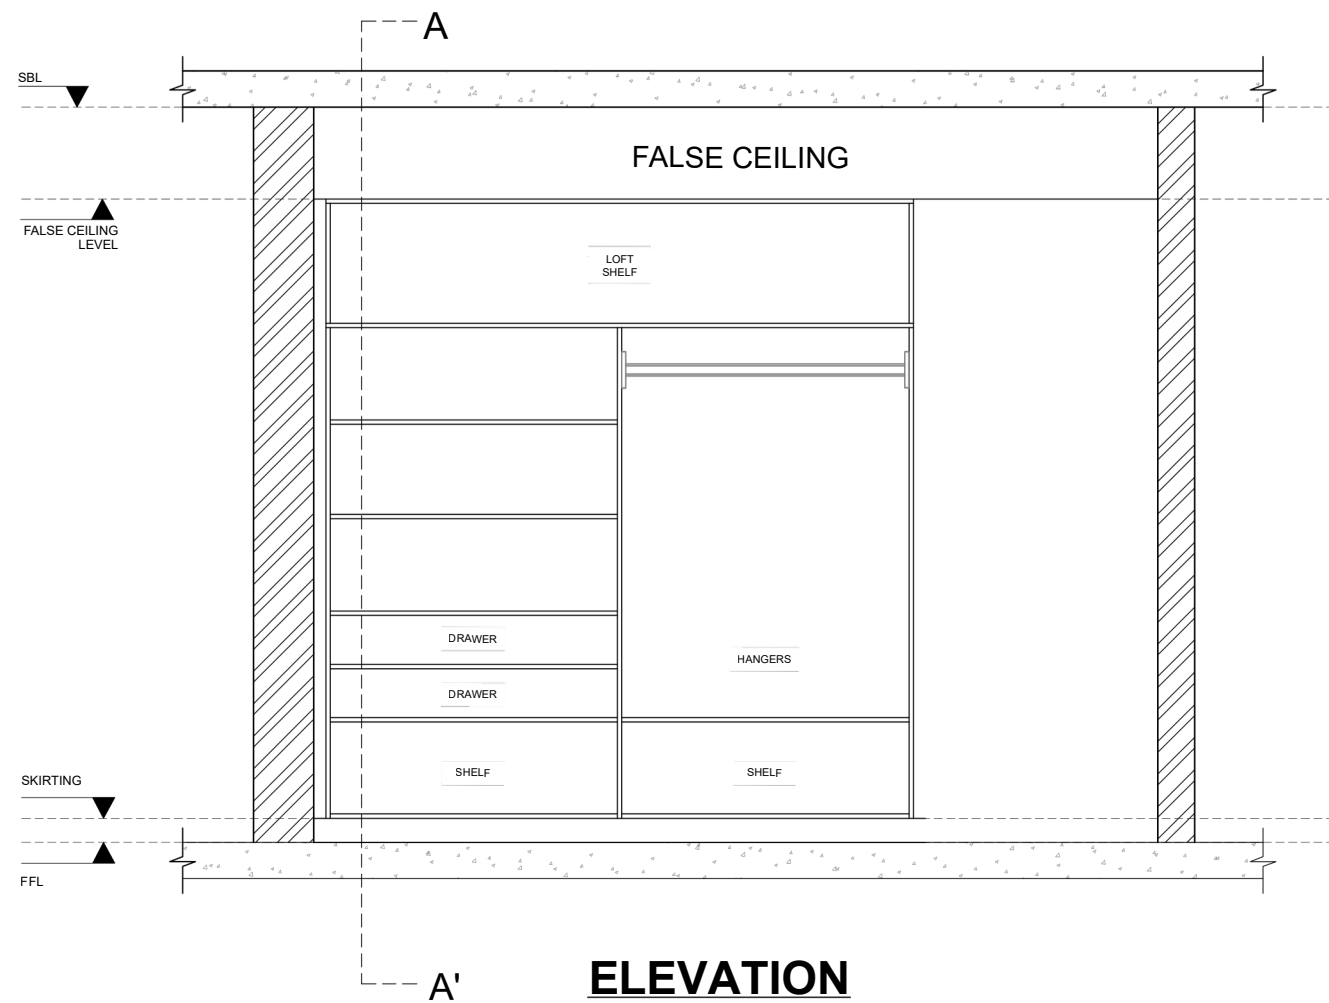


ELEVATION

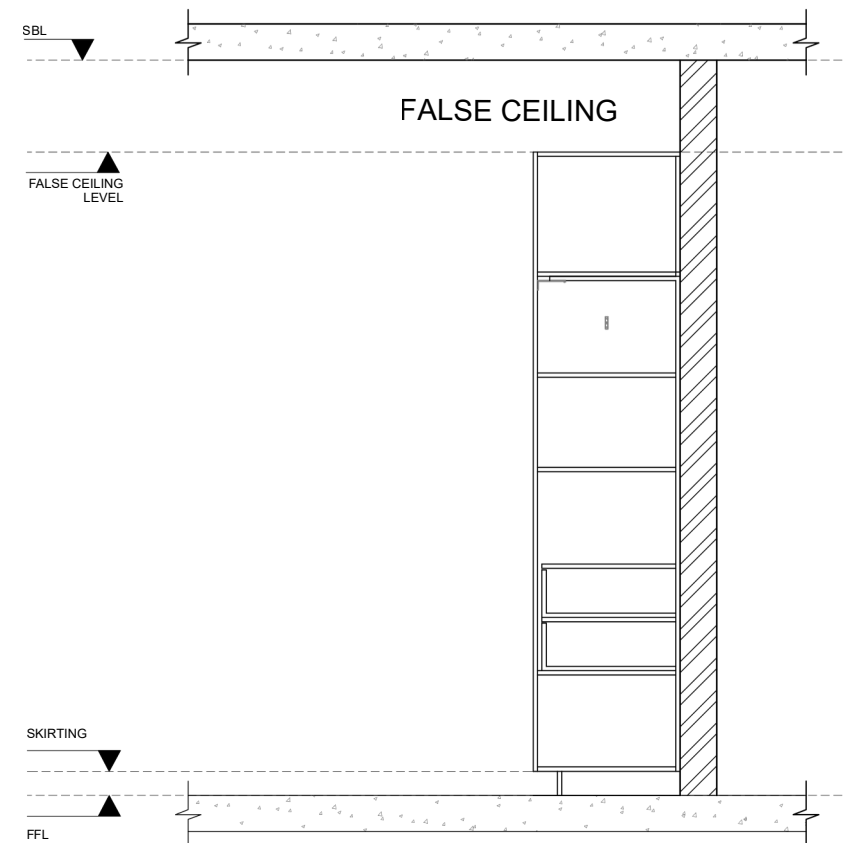

SECTION AA'

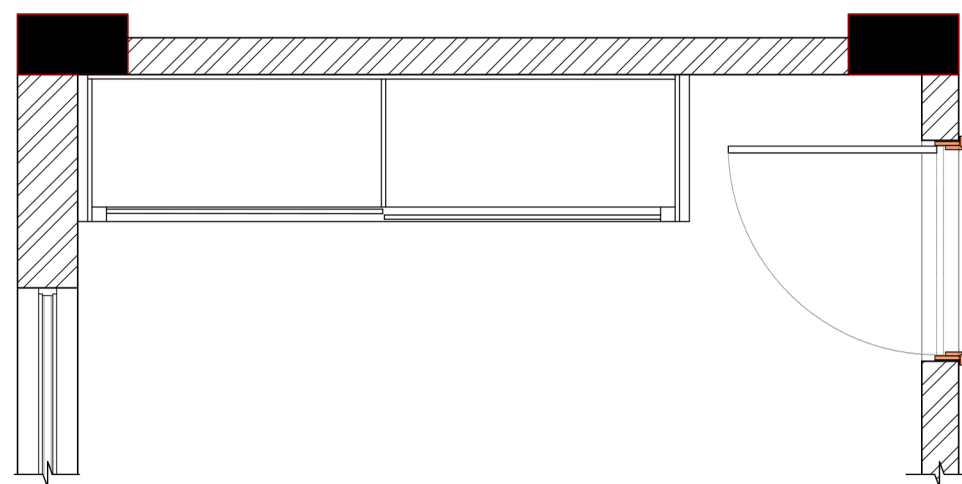


PLAN

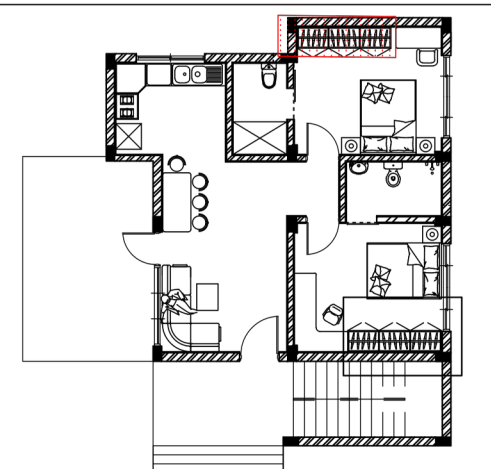

KEY PLAN

07

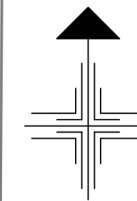

NOTES:

1. DIMENSIONS TO BE CHECKED AS PER SITE CONDITION.
2. ALL DIMENSIONS ARE IN FT AND INCHES UNLESS MENTIONED
3. DRAWINGS ARE TO BE READ AND NOT TO BE SCALED
4. ARCHITECT MUST BE NOTIFIED IF ANY DISCREPANCY OCCURS BETWEEN THE DRAWING AND THE SITE BEFORE STARTING THE WORK

DRAWN: POTLURI CHINMAYI

ROLL NO: 22WU0301110



PROGRAM: INTERIOR DESIGN SEM-V

DATE: 20-08-2024


SCALE: N.T.S.

SHEET TITLE: WALL ELEVATION

PROJECT TITLE: 2BHK VILLA

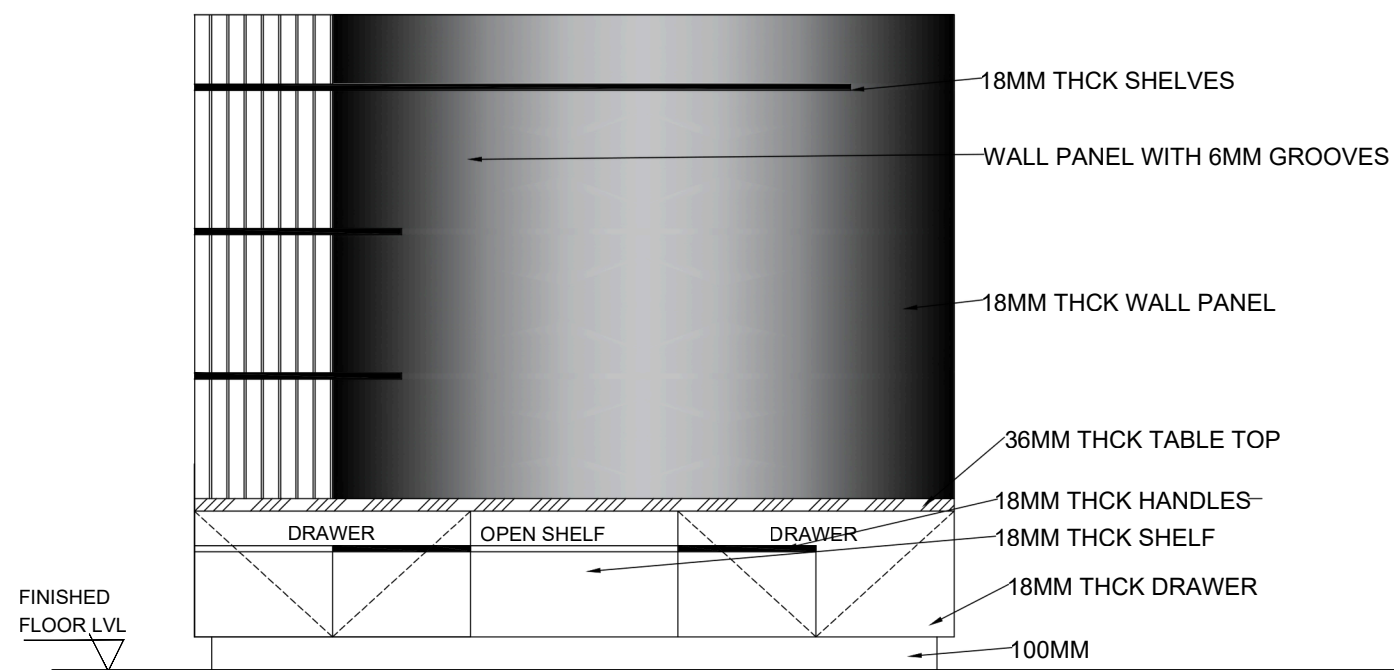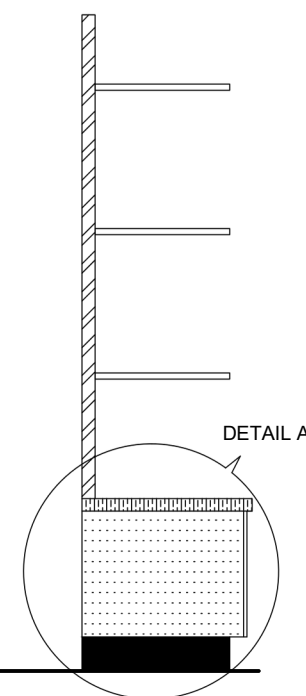FRONT
ELEVATION


SECTION

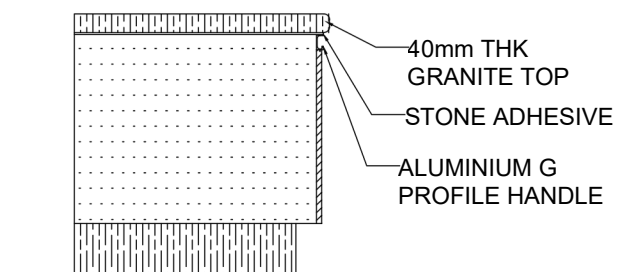


DETAIL A




PLAN

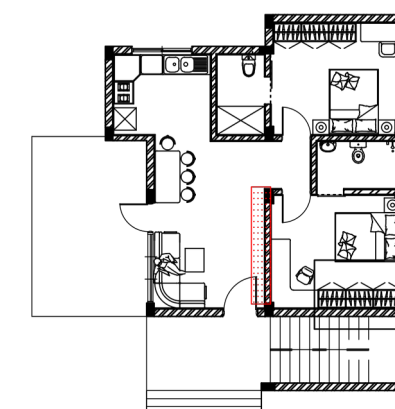


KEY PLAN

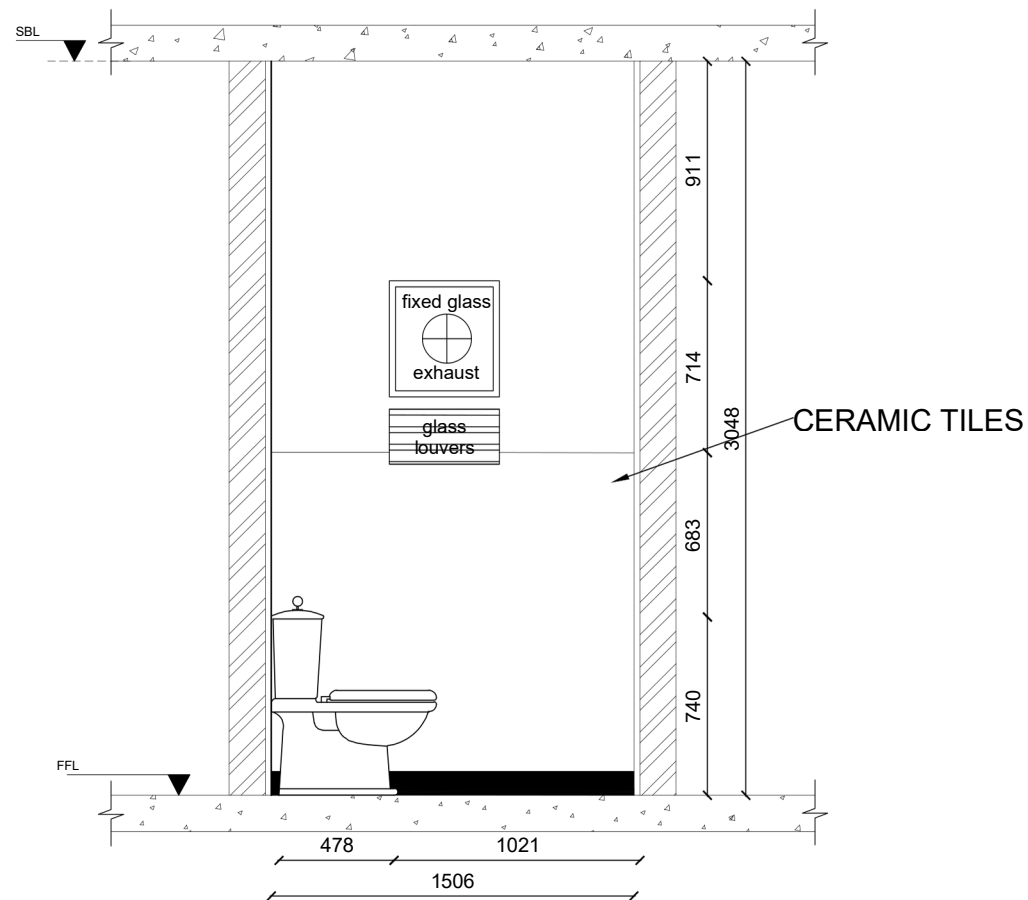


**SECTIONAL
ELEVATION**

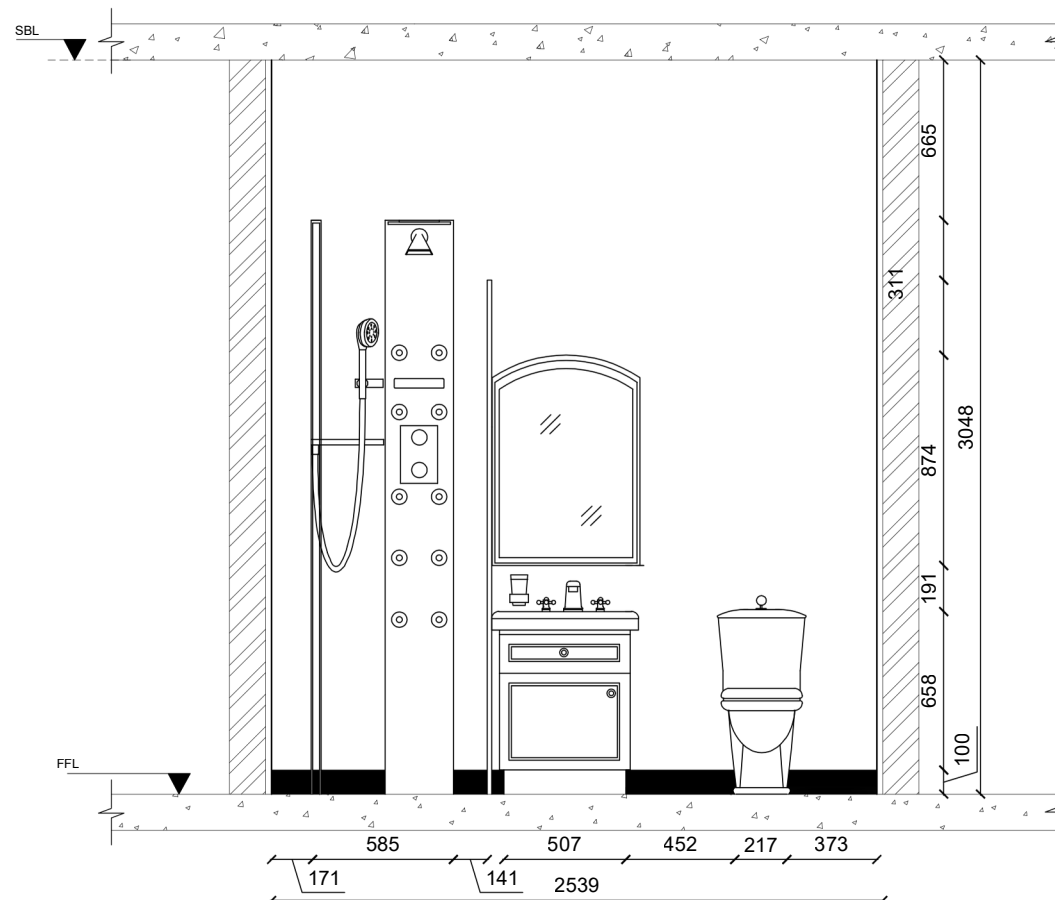

**SECTIONAL
ELEVATION**

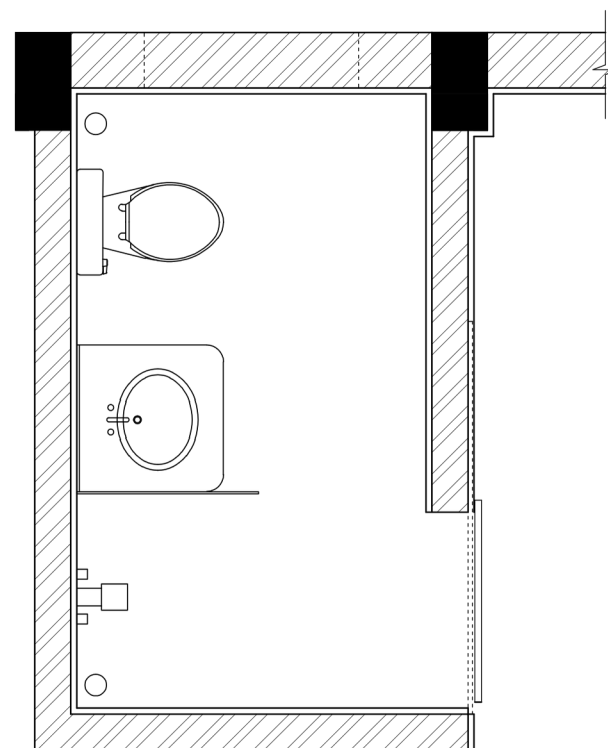


PLAN

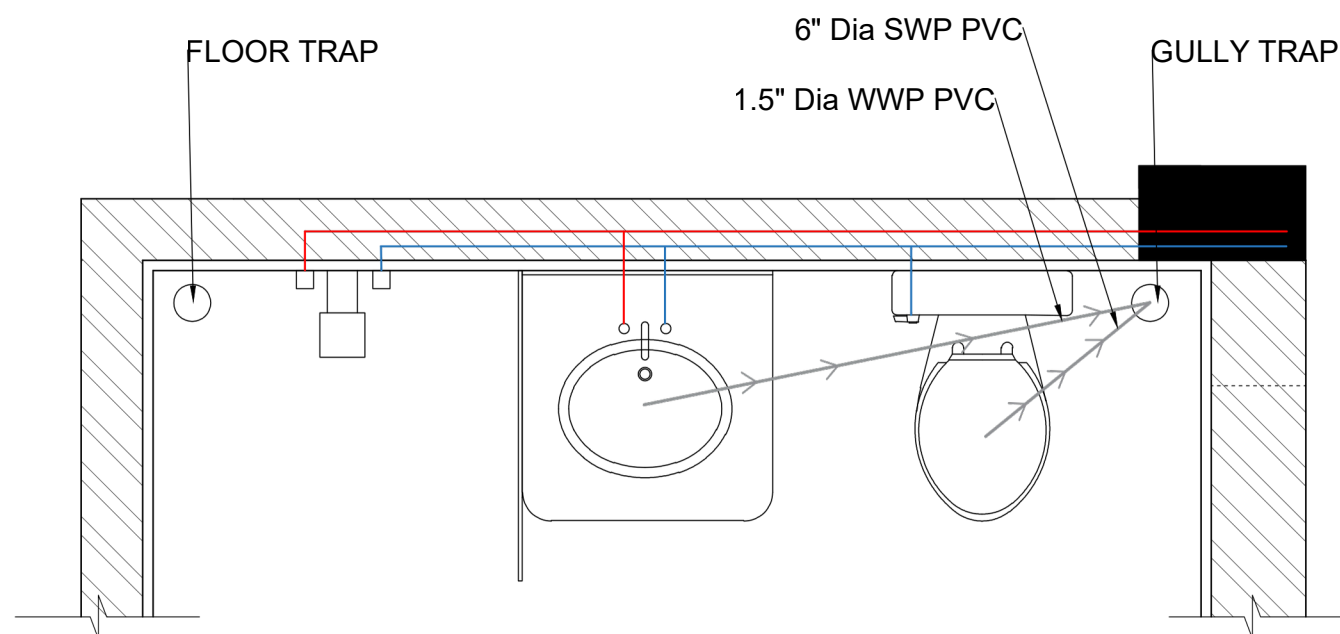

PLUMBING

08

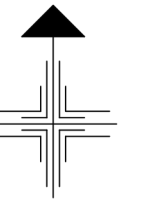

NOTES:

1. DIMENSIONS TO BE CHECKED AS PER SITE CONDITION.
2. ALL DIMENSIONS ARE IN FT AND INCHES UNLESS MENTIONED
3. DRAWINGS ARE TO BE READ AND NOT TO BE SCALED
4. ARCHITECT MUST BE NOTIFIED IF ANY DISCREPANCY OCCURS BETWEEN THE DRAWING AND THE SITE BEFORE STARTING THE WORK

DRAWN: POTLURI CHINMAYI

ROLL NO: 22WU0301110


PROGRAM: INTERIOR DESIGN SEM-V

DATE: 20-08-2024




SCALE: N.T.S.

SHEET TITLE: BATHROOM DETAIL


PROJECT TITLE: 2BHK VILLA

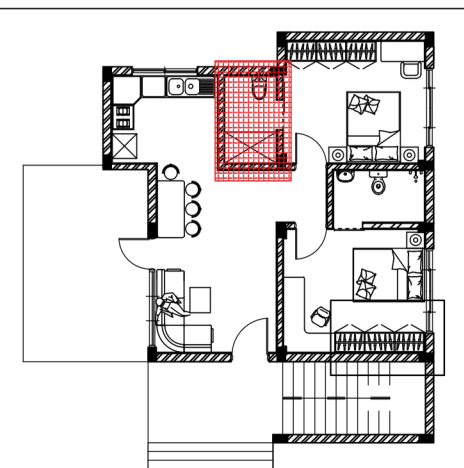

KEY PLAN

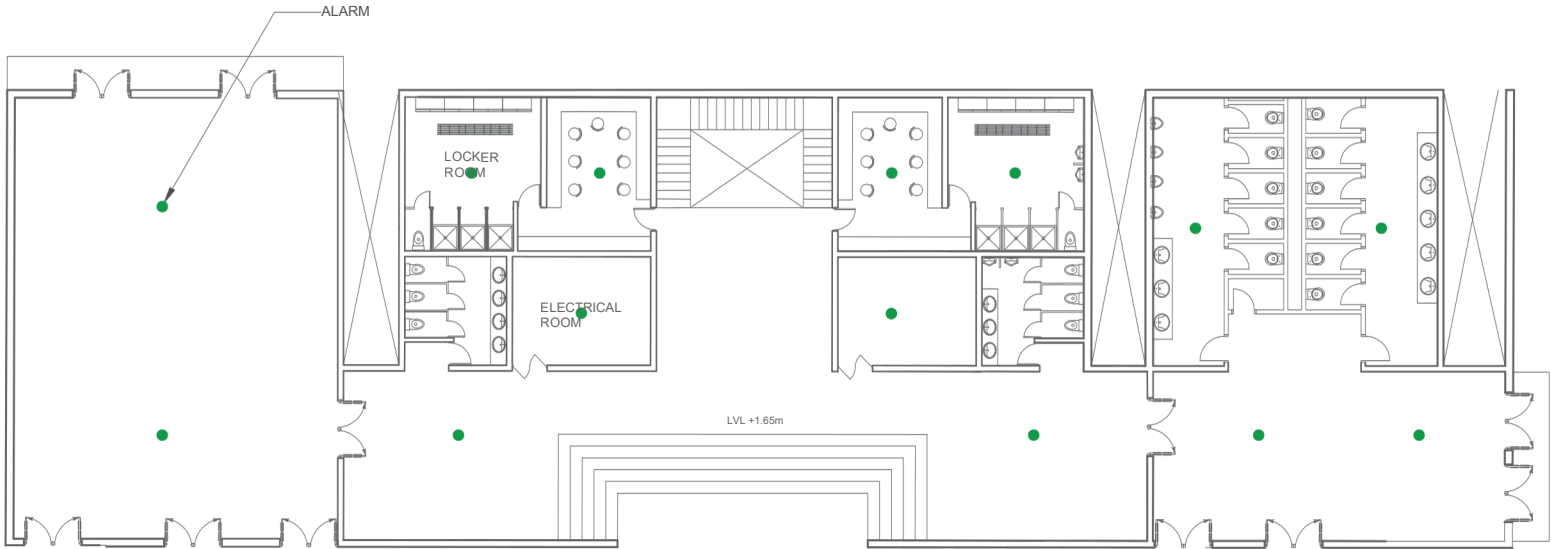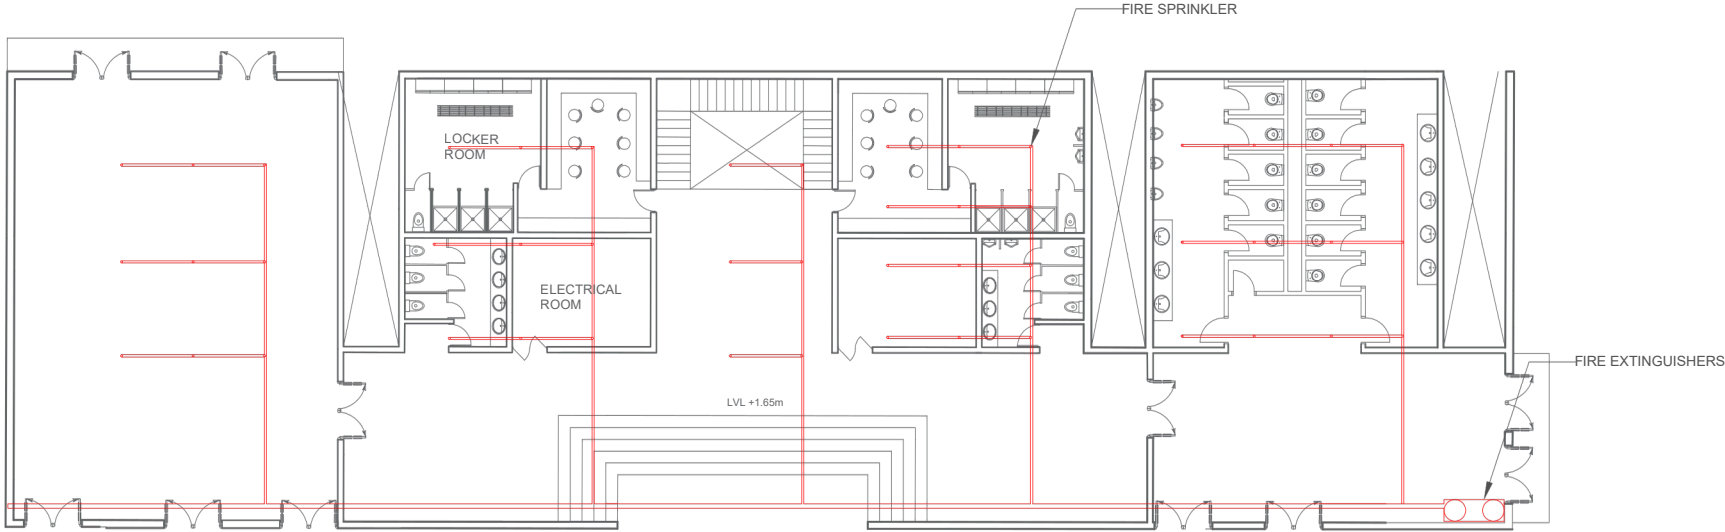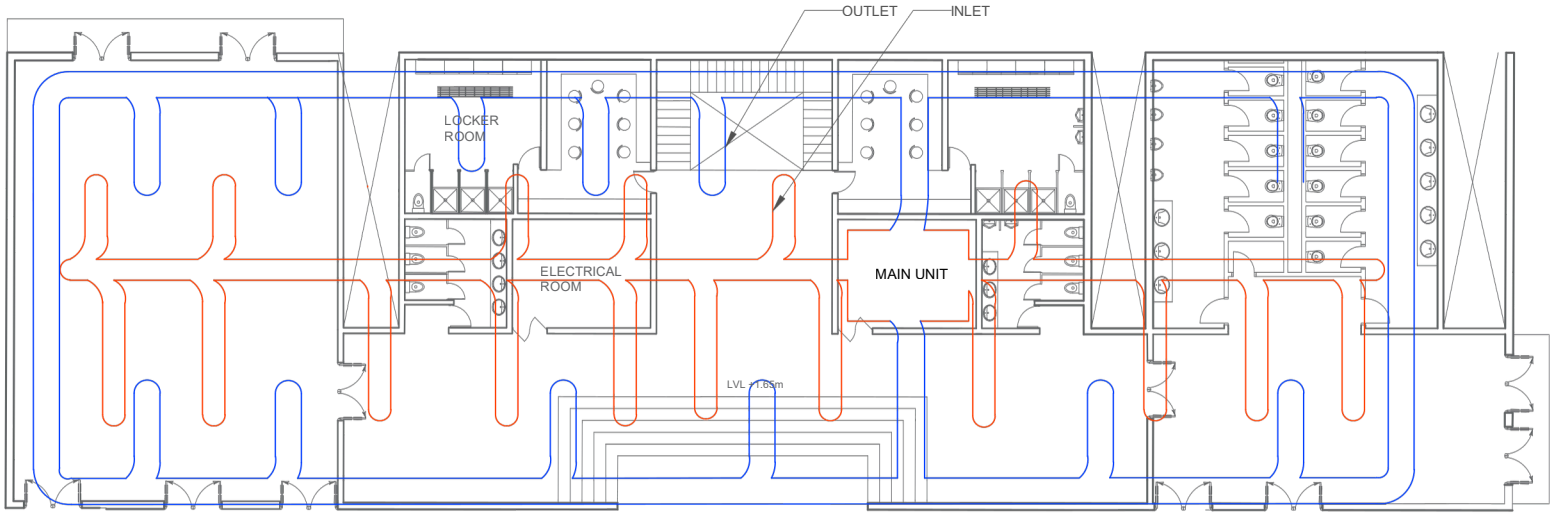

09

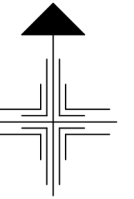

NOTES:

1. DIMENSIONS TO BE CHECKED AS PER SITE CONDITION.
2. ALL DIMENSIONS ARE IN FT AND INCHES UNLESS MENTIONED
3. DRAWINGS ARE TO BE READ AND NOT TO BE SCALED
4. ARCHITECT MUST BE NOTIFIED IF ANY DISCREPANCY OCCURS BETWEEN THE DRAWING AND THE SITE BEFORE STARTING THE WORK

DRAWN: POTLURI CHINMAYI

ROLL NO: 22WU0301110

PROGRAM: INTERIOR DESIGN SEM-V


DATE: 20-08-2024

SCALE: N.T.S.

SHEET TITLE: SERVICES


PROJECT TITLE: 2BHK VILLA

KEY PLAN

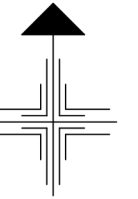

NOTES:

1. DIMENSIONS TO BE CHECKED AS PER SITECONDITION.
2. ALL DIMENSIONS ARE IN FT AND INCHES UNLESS MENTIONED
3. DRAWINGSARETOBEREADANDNOT TOBESCALED
4. ARCHITECT MUST BE NOTIFIED IF ANY DISCREPANCY OCCURS BETWEEN THE DRAWING AND THE SITE BEFORE STARTING THE WORK

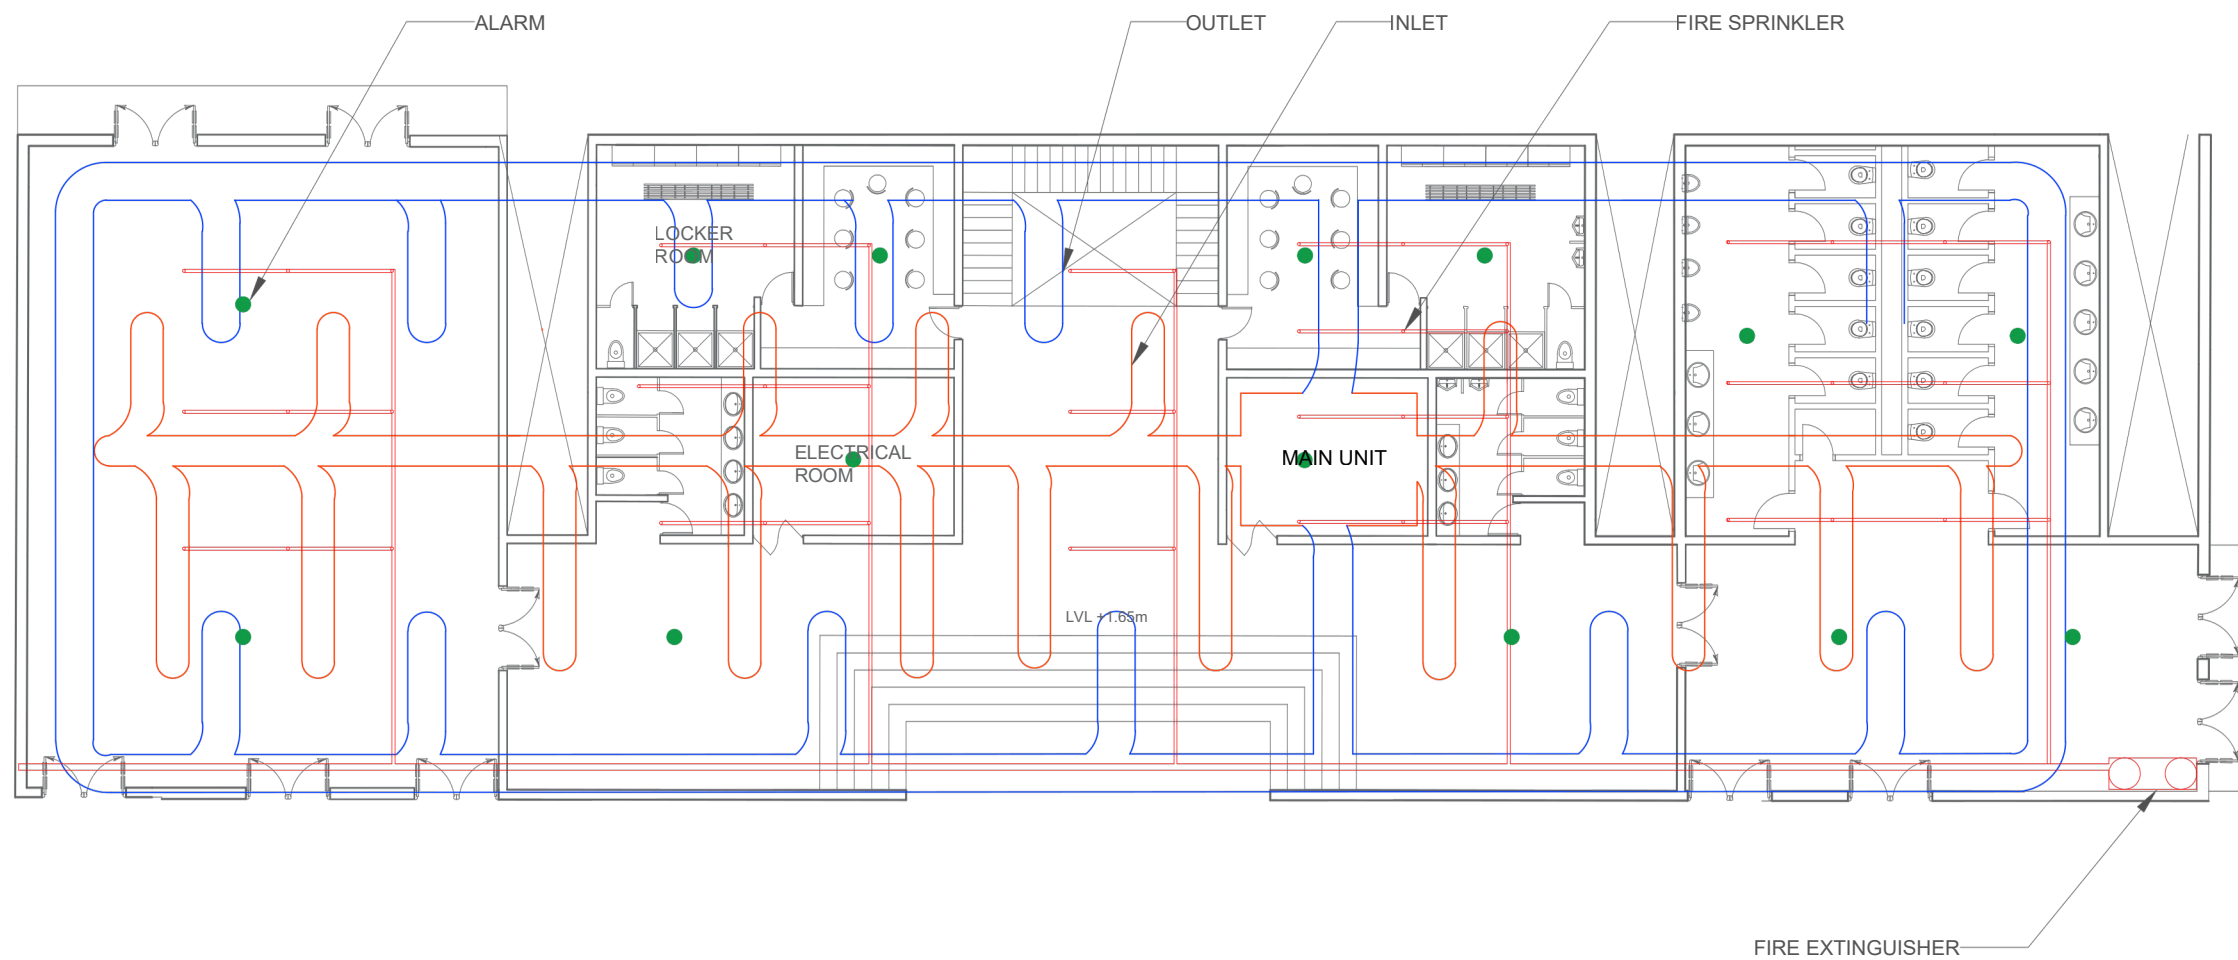

DRAWN: POTLURICHINMAYI

ROLL NO: 22WU0301110


PROGRAM: INTERIORDESIGN SEM-V

DATE: 20-08-2024


SCALE: N.T.S.

SHEET TITLE: SERVICES

PROJECT TITLE: BACKSTAGE

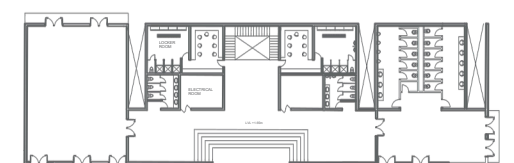

KEY PLAN

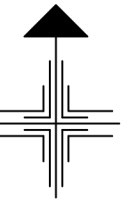

NOTES:

- 1. DIMENSIONS TO BE CHECKED AS PER SITE CONDITION.
- 2. ALL DIMENSIONS ARE IN FT AND INCHES UNLESS MENTIONED
- 3. DRAWINGS ARE TO BE READ AND NOT TO BE SCALED
- 4. ARCHITECT MUST BE NOTIFIED IF ANY DISCREPANCY OCCURS BETWEEN THE DRAWING AND THE SITE BEFORE STARTING THE WORK

DRAWN: POTLURI CHINMAYI

ROLL NO: 22WU0301110

PROGRAM: INTERIOR DESIGN SEM-V


DATE: 09-08-2024


SCALE: N.T.S.

SHEET TITLE: FURNITURE LAYOUT

PROJECT TITLE: G+3 VILLA

SIGNATURE

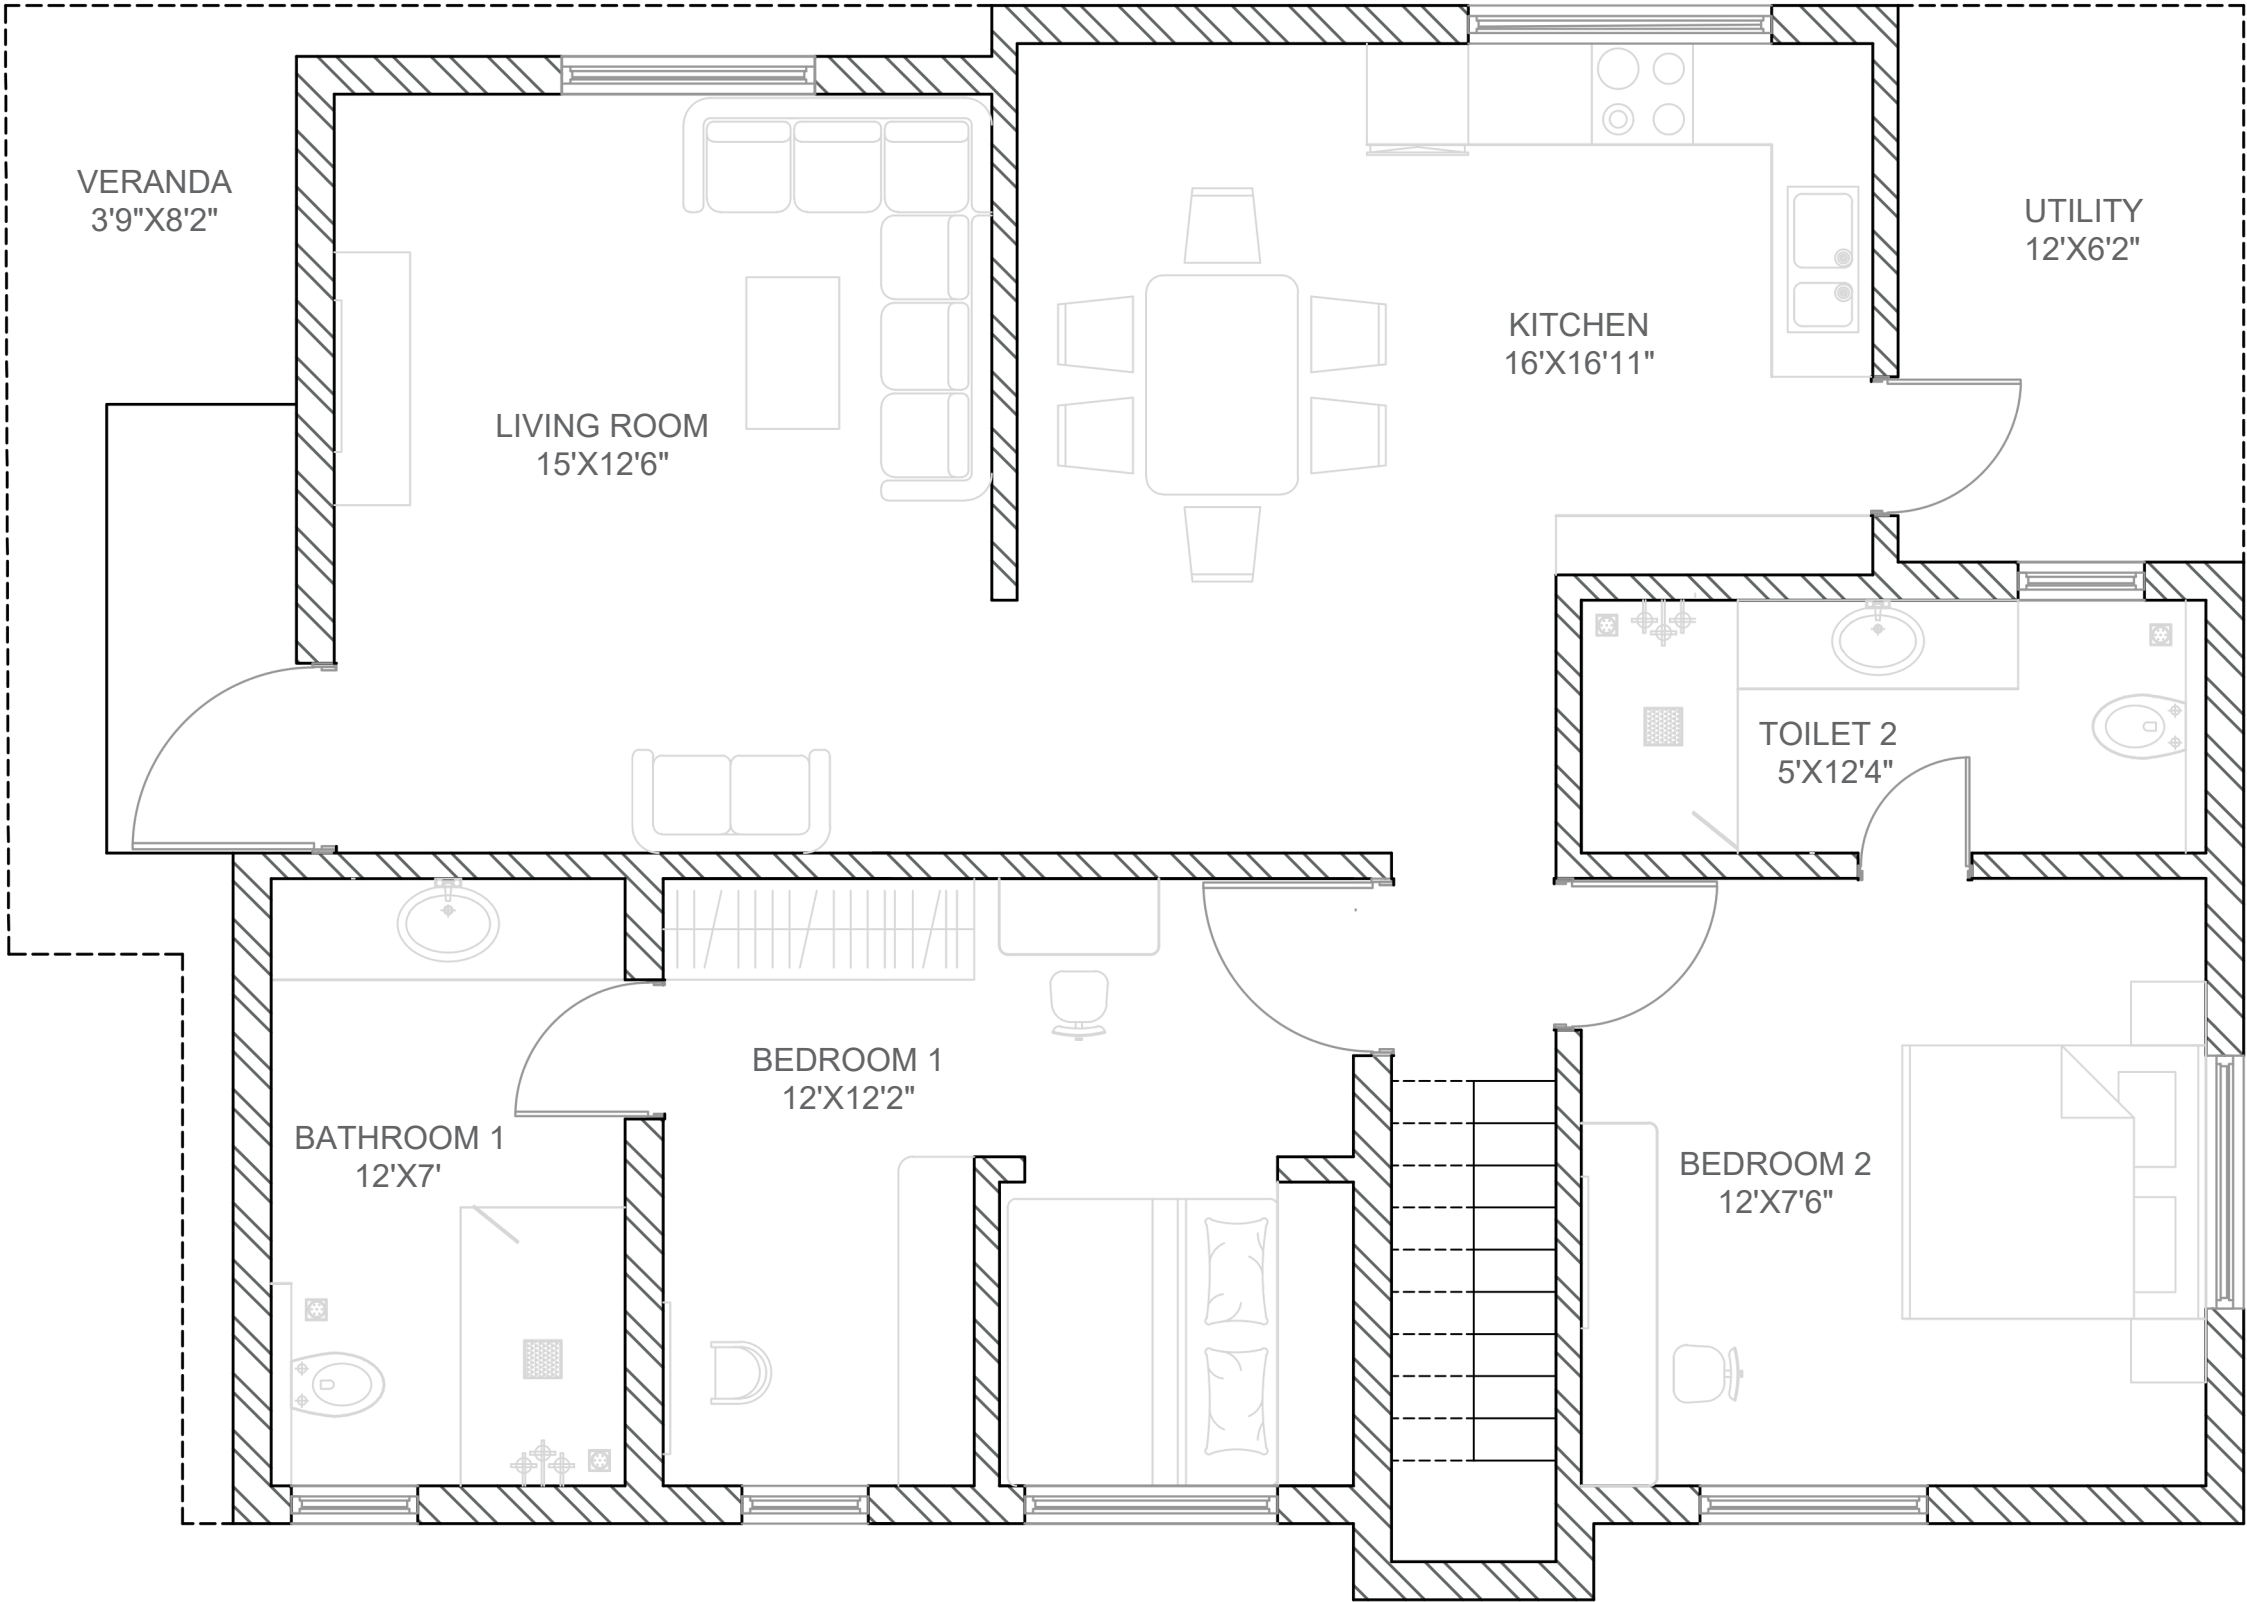

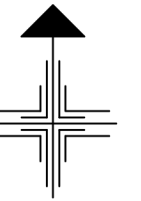

NOTES:

- 1. DIMENSIONS TO BE CHECKED AS PER SITE CONDITION.
- 2. ALL DIMENSIONS ARE IN FT AND INCHES UNLESS MENTIONED
- 3. DRAWINGS ARE TO BE READ AND NOT TO BE SCALED
- 4. ARCHITECT MUST BE NOTIFIED IF ANY DISCREPANCY OCCURS BETWEEN THE DRAWING AND THE SITE BEFORE STARTING THE WORK

DRAWN: POTLURI CHINMAYI

ROLL NO: 22WU0301110


PROGRAM: INTERIOR DESIGN SEM-V

DATE: 09-08-2024


SCALE: N.T.S.

SHEET TITLE: REFLECTED CEILING PLAN

PROJECT TITLE: G+3 VILLA

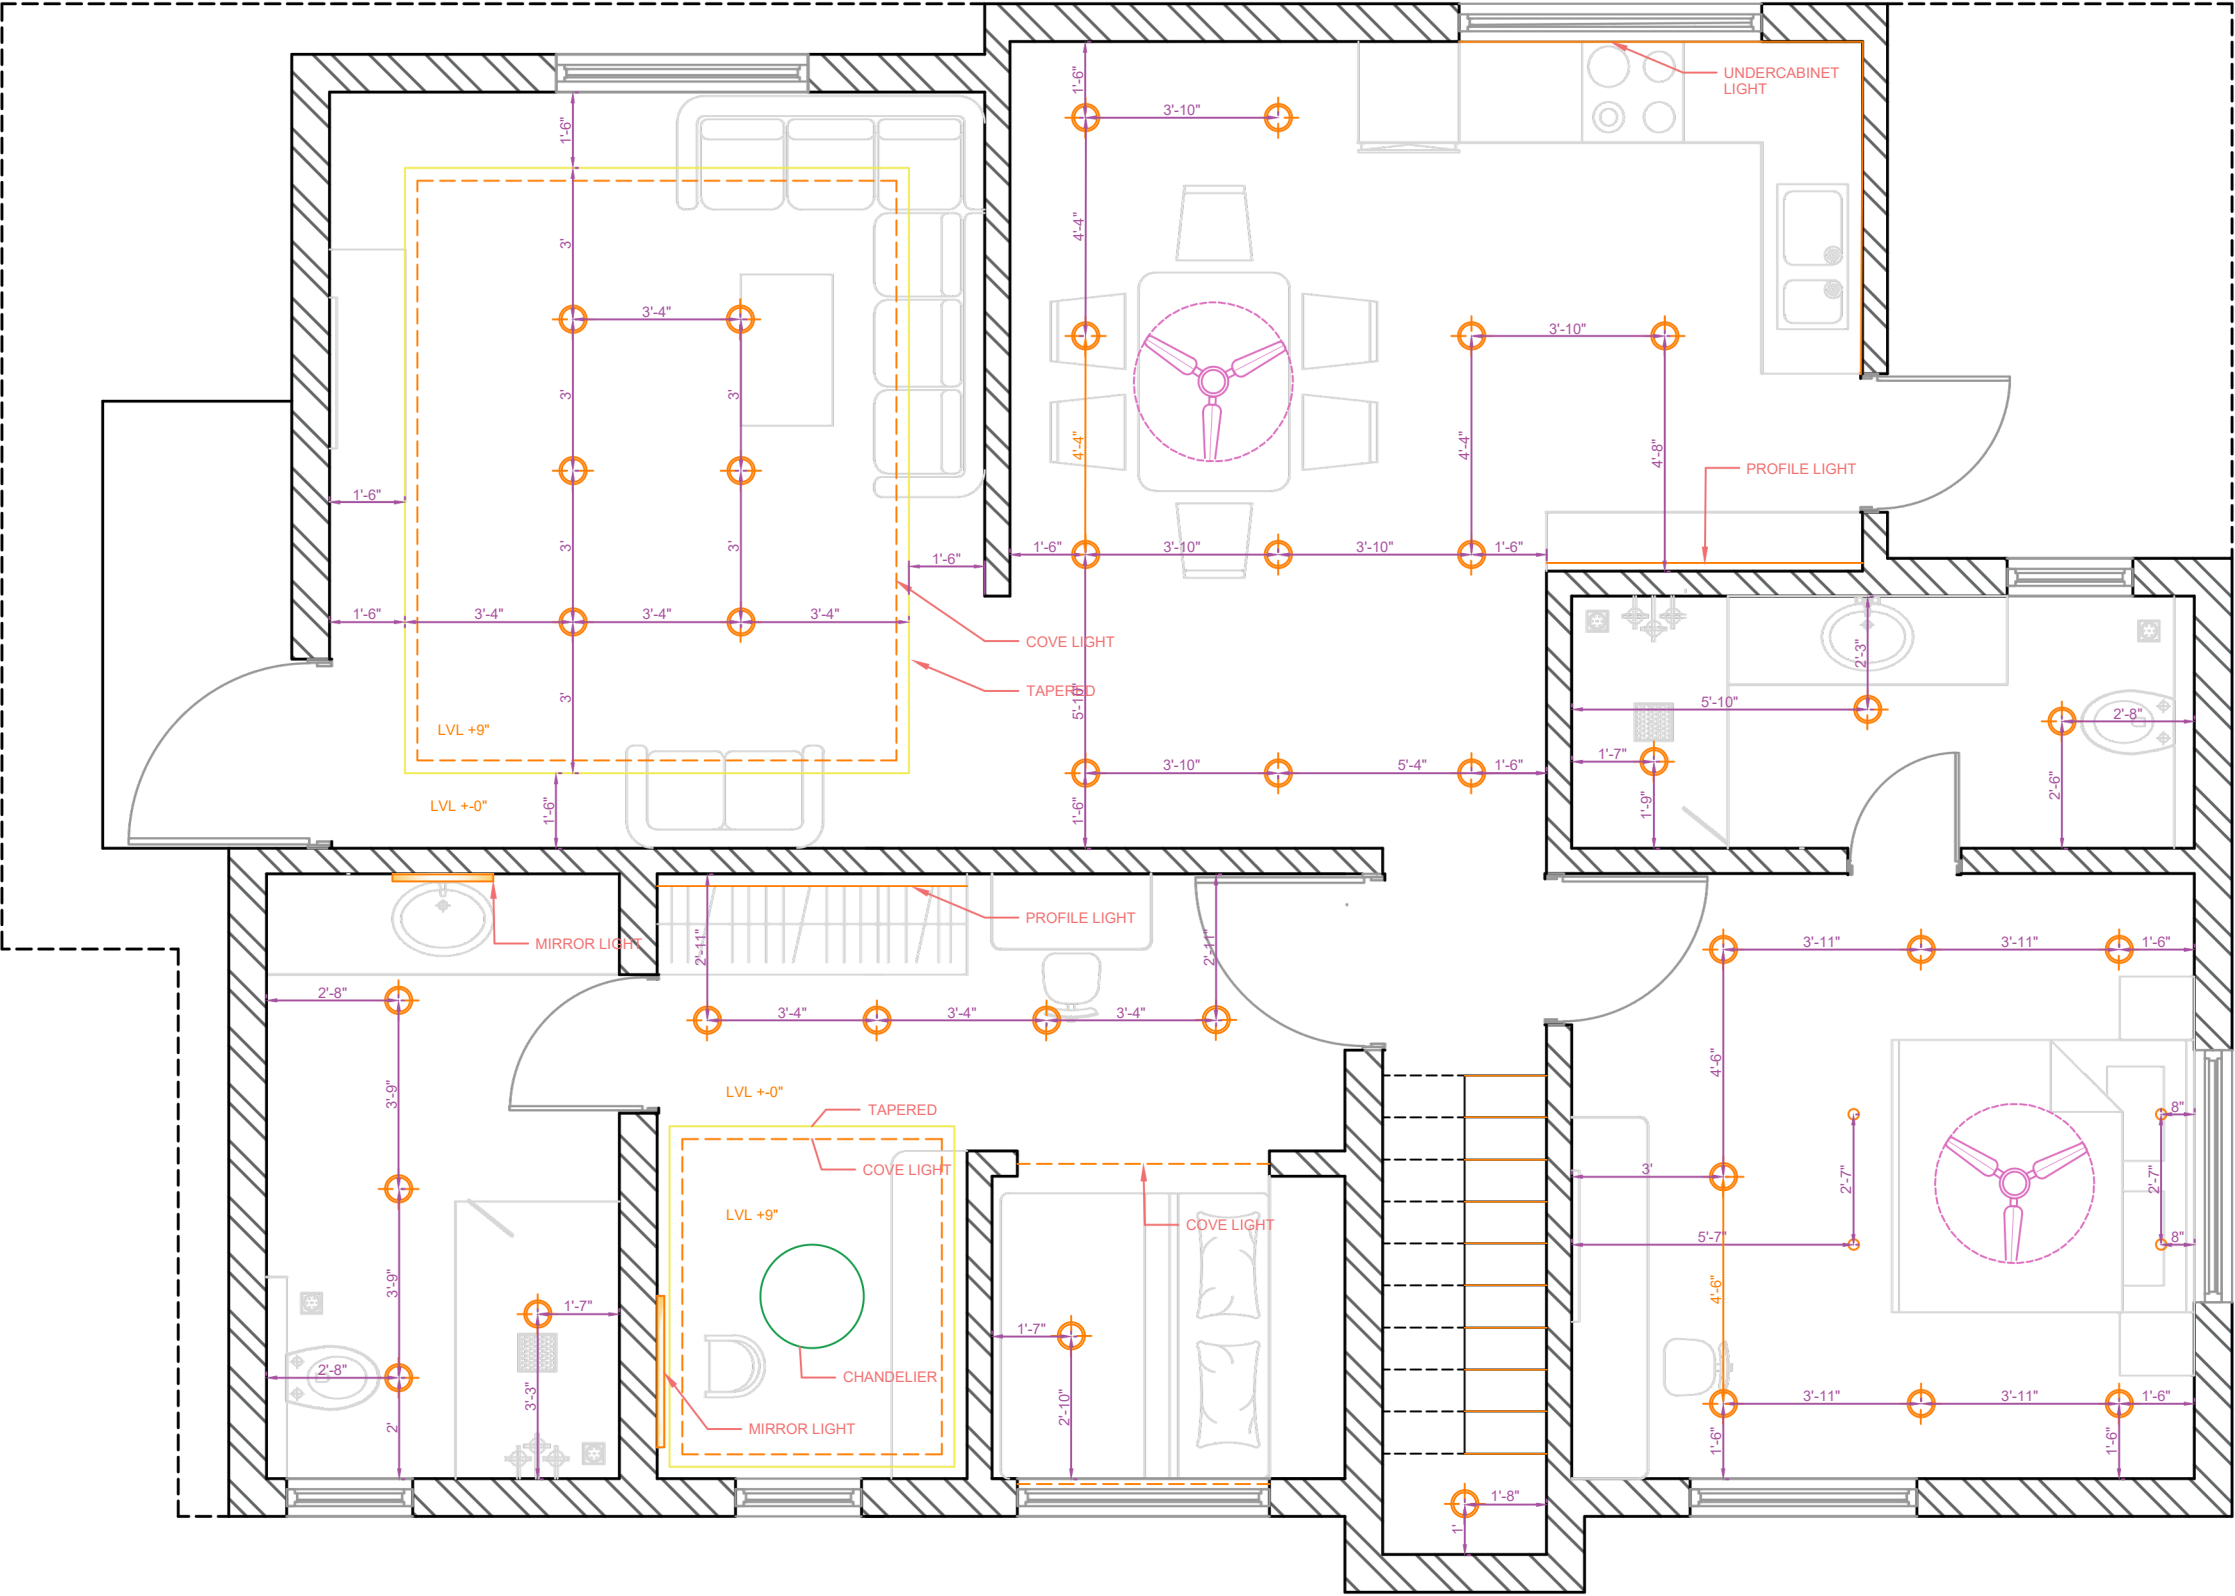

SIGNATURE

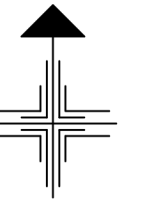

NOTES:

- 1. DIMENSIONS TO BE CHECKED AS PER SITE CONDITION.
- 2. ALL DIMENSIONS ARE IN FT AND INCHES UNLESS MENTIONED
- 3. DRAWINGS ARE TO BE READ AND NOT TO BE SCALED
- 4. ARCHITECT MUST BE NOTIFIED IF ANY DISCREPANCY OCCURS BETWEEN THE DRAWING AND THE SITE BEFORE STARTING THE WORK

DRAWN: POTLURI CHINMAYI

ROLL NO: 22WU0301110


PROGRAM: INTERIOR DESIGN SEM-V

DATE: 09-08-2024

SCALE: N.T.S.

SHEET TITLE: ELECTRICAL LOOPING

PROJECT TITLE: G+3 VILLA

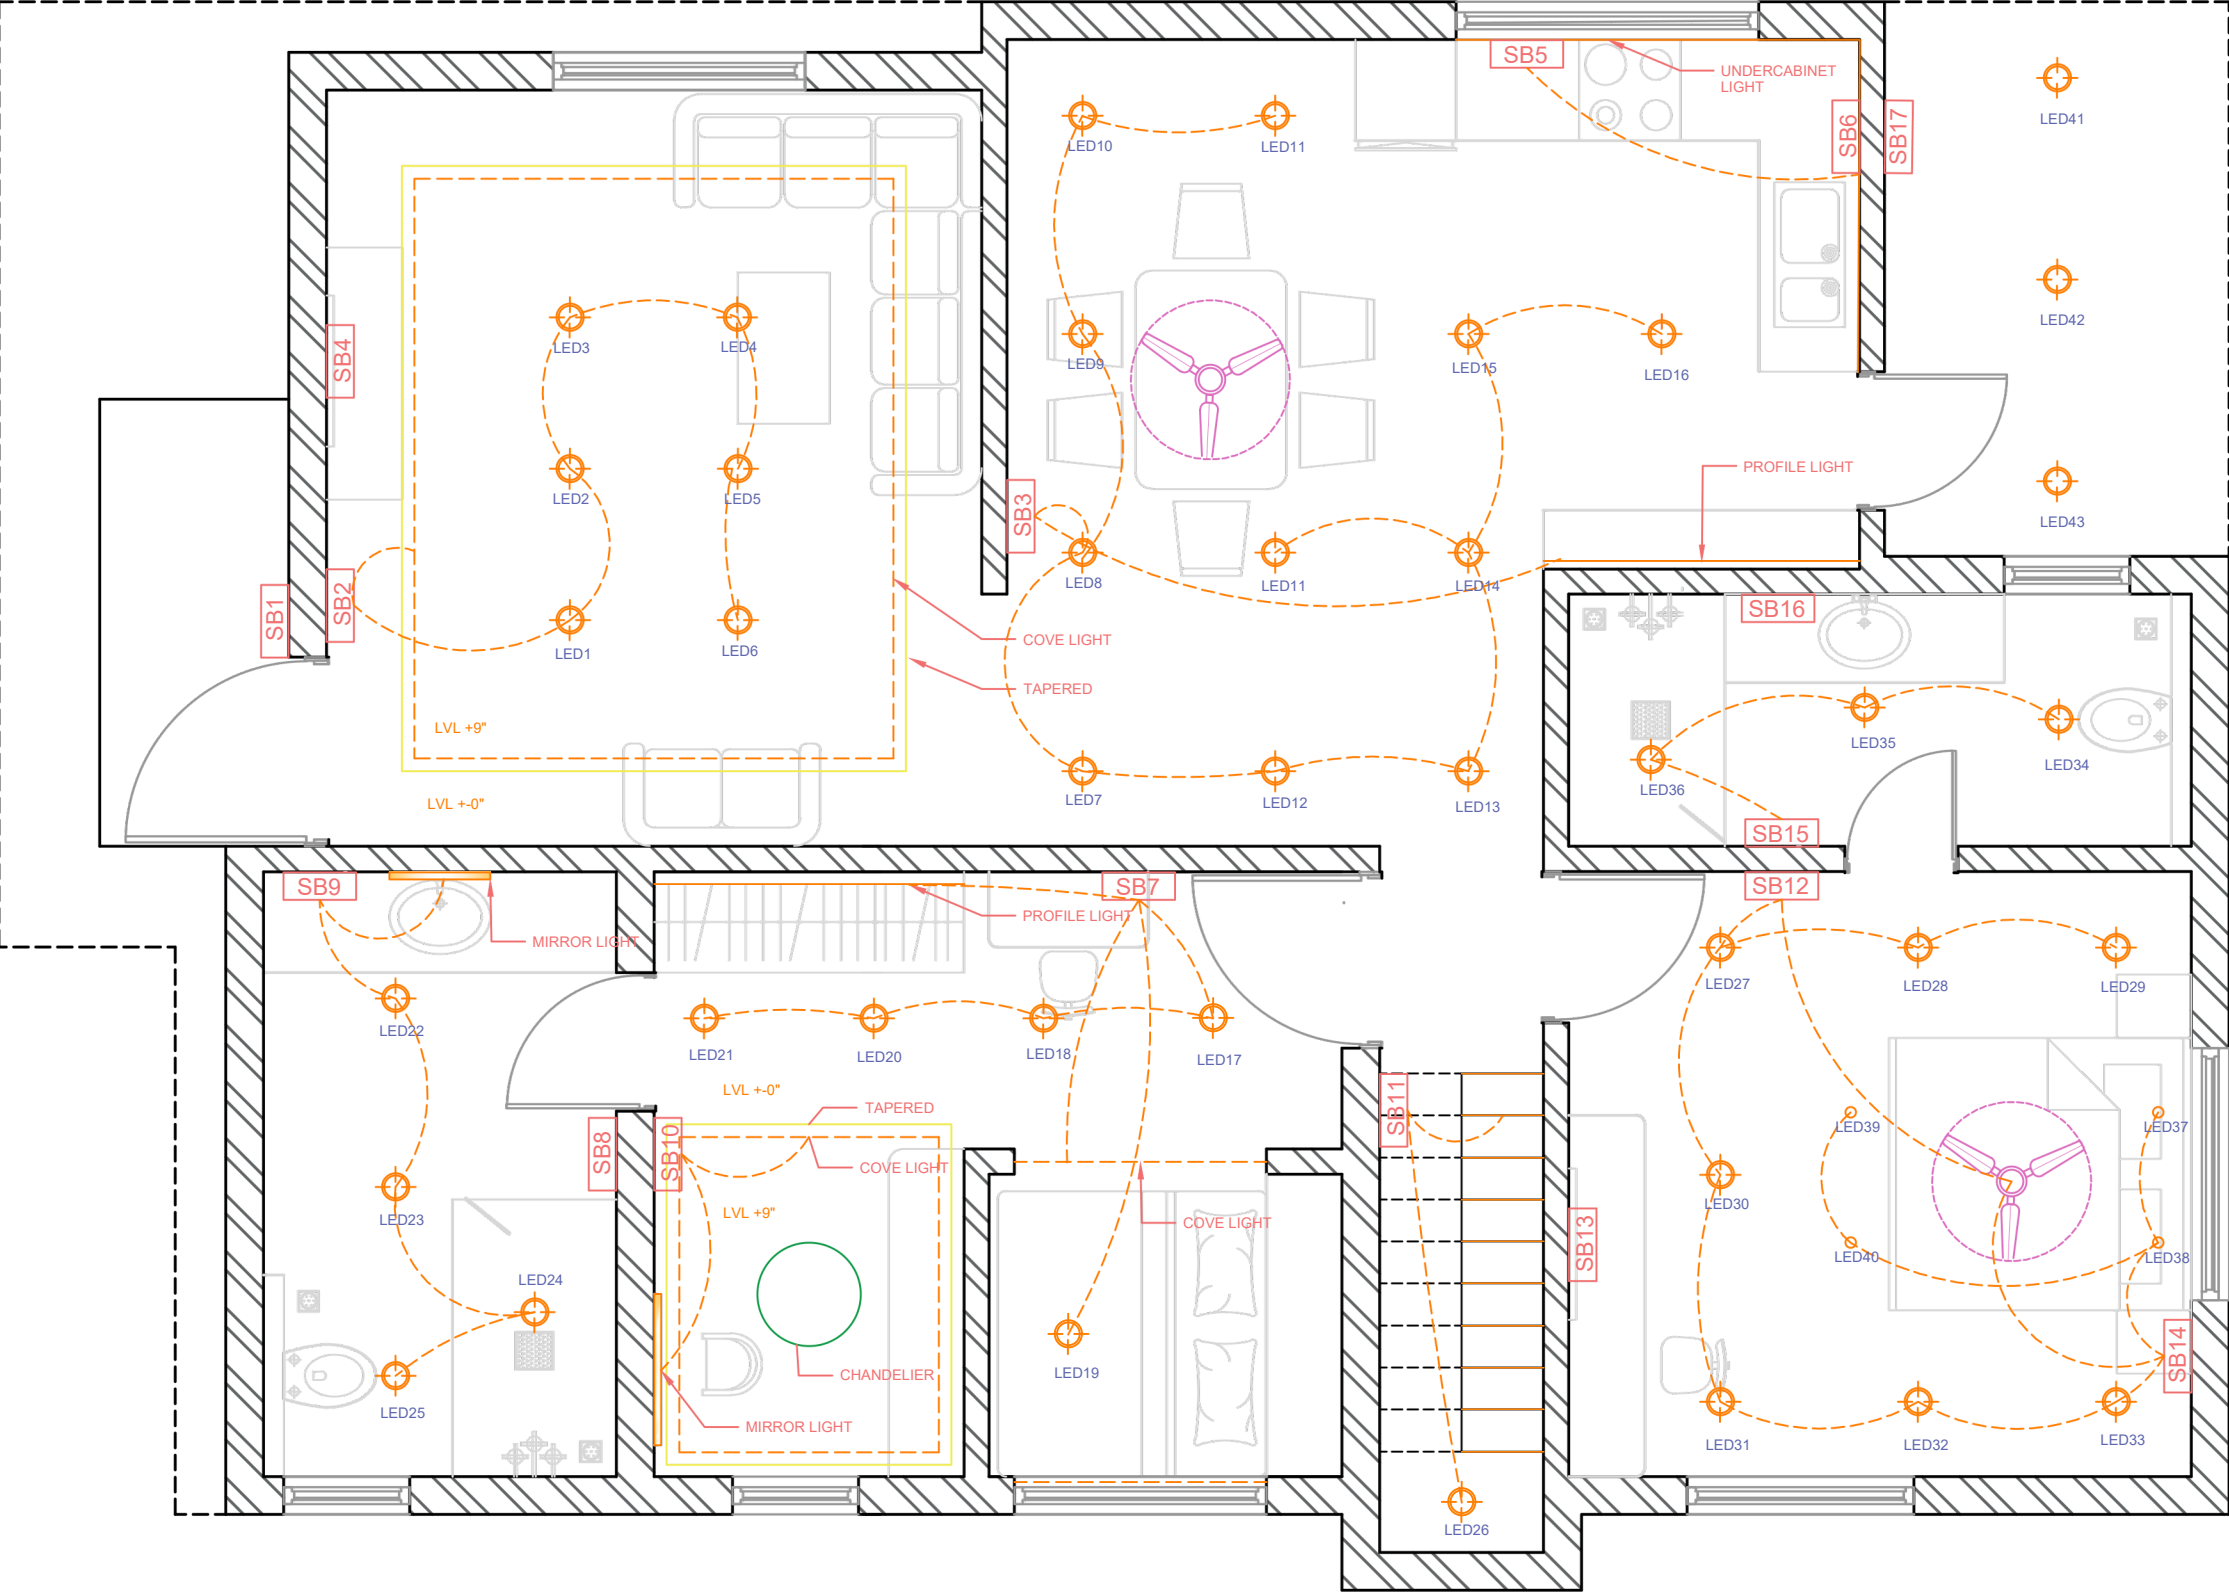

SIGNATURE

SB1	HEIGHT 48" FFL (1 MODULE)
MAIN DOOR ENTRY	
SW1	BELL PUSH (ON/OFF)

SB2	HEIGHT 48" FFL (7 MODULE)
LIVING ROOM	
SW1	LED1, LED2, LED3, LED4, LED5, LED6
SW2	COVE LIGHT
SW3	5 AMP P/P
SW3	5 AMP P/P
SW4	ON/OFF FOR 5 AMP P/P
SW5	ON/OFF FOR 5 AMP P/P

SB3	HEIGHT 48" FFL (4 MODULE)
DINING ROOM	
SW1	LED7, LED8, LED9, LED10, LED11, LE12, LE13, LED14, LED15, LED16
SW2	FAN
1 NO	REGUALTOR
SW3	DIFFUSE LIGHT
1 NO	6 AND 16 AMP P/P
SW3	ON/OFF FOR 6 AND 16 AMP P/P

SB4	HEIGHT 24" FFL (4 MODULE)
LIVING ROOM	
2 NO	6 AND 16 AMP P/P
SW1	ON/OFF FOR 5 AMP P/P
SW2	ON/OFF FOR 5 AMP P/P
SW3	ON/OFF FOR 5 AMP P/P
1 NO	T.V.CABLE POINT

SB5	HEIGHT 48" FFL (3 MODULE)
KITCHEN	
SW1	DIFFUSE LIGHT (UNDER CABINET)
1 NO	5 AMP P/P
SW4	ON/OFF FOR 5 AMP P/P

SB6	HEIGHT 48" FFL (1 MODULE)
KITCHEN	
1 NO	16 AMP P/P
SW1	ON/OFF FOR 16 AMP P/P

SB7	HEIGHT 48" FFL (5 MODULE)
BEDROOM 1	
SW1	LED17, LED19, LED20, LED 21
SW2	LED18, COVE LIGHT, PROFILE
1 NO	5 AMP P/P
SW3	ON/OFF FOR 5 AMP P/P

SB8	HEIGHT 48" FFL (2 MODULE)
BATHROOM 2	
SW1	LED22, LED23, LED24, LED25
SW2	GEYSER
SW3	EXHAUST FAN

SB9	HEIGHT 48" FFL (2 MODULE)
BATHROOM 1	
SW1	MIRROR LIGHT
2 NO	5 AMP P/P
SW2	ON/OFF FOR 5 AMP P/P
SW3	ON/OFF FOR 5 AMP P/P

SB10	HEIGHT 48" FFL (5 MODULE)
DRESSING ROOM	
SW1	COVE LIGHT
SW2	MIRROR LIGHT
1 NO	5 AMP P/P
SW3	ON/OFF FOR 5 AMP P/P

SB11	HEIGHT 48" FFL (1 MODULE)
STAIRWAY	
SW1	PROFILE LIGHT
SW2	LED26

SB12	HEIGHT 24" FFL (4 MODULE)
BEDROOM 2	
SW1	LED27, LED28, LED29, LED30, LED31, LED32, LED33 (TWO WAY FROM SB14)
SW2	FAN (TWO WAY FROM SB14)
1 NO	REGULATOR
1 NO	5 AMP P/P
SW4	ON/OFF FOR 5 AMP P/P
SW5	USB POINT FOR MOBILE CHARGER

SB13	HEIGHT 24" FFL (4 MODULE)
LIVING ROOM	
2 NO	6 AND 16 AMP P/P
SW1	ON/OFF FOR 5 AMP P/P
SW2	ON/OFF FOR 5 AMP P/P
SW3	ON/OFF FOR 5 AMP P/P
1 NO	T.V.CABLE POINT


SB14	HEIGHT 48" FFL (3 MODULE)
BEDROOM 2	
SW1	LED27, LED28, LED29, LED30, LED31, LED32, LED33 (TWO WAY FROM SB12)
SW2	FAN (TWO WAY FROM SB12)
1 NO	REGULATOR
1 NO	5 AMP P/P
SW3	ON/OFF FOR 5 AMP P/P
SW4	LED37, LED 38, LED39, LED 40

SB15	HEIGHT 48" FFL (2 MODULE)
BATHROOM 2	
SW1	LED34, LED35, LED36
SW2	GEYSER
SW3	EXHAUST FAN

SB16	HEIGHT 48" FFL (2 MODULE)
BATHROOM 2	
2 NO	5 AMP P/P
SW2	ON/OFF FOR 5 AMP P/P
SW3	ON/OFF FOR 5 AMP P/P

SB17	HEIGHT 48" FFL (1 MODULE)
UTILITY	
SW1	NO 1 15 AMP P/P FOR WASHING MACHINE
SW2	SW 1 ON/OFF FOR 15 AMP P/P IN S.B.17

04

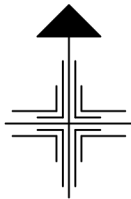

NOTES:

- DIMENSIONS TO BE CHECKED AS PER SITE CONDITION.
- ALL DIMENSIONS ARE IN FT AND INCHES UNLESS MENTIONED
- DRAWINGS ARE TO BE READ AND NOT TO BE SCALED
- ARCHITECT MUST BE NOTIFIED IF ANY DISCREPANCY OCCURS BETWEEN THE DRAWING AND THE SITE BEFORE STARTING THE WORK

DRAWN: POTLURI CHINMAYI

ROLL NO: 22WU0301110

PROGRAM: INTERIOR DESIGN SEM-V


DATE: 20-08-2024

SCALE: N.T.S.

SHEET TITLE: SWITCH BOARD SPECS.

PROJECT TITLE: G+3 VILLA

SIGNATURE

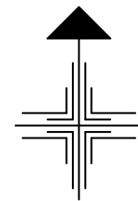

NOTES:

1. DIMENSIONS TO BE CHECKED AS PER SITE CONDITION.
2. ALL DIMENSIONS ARE IN FT AND INCHES UNLESS MENTIONED
3. DRAWINGS ARE TO BE READ AND NOT TO BE SCALED
4. ARCHITECT MUST BE NOTIFIED IF ANY DISCREPANCY OCCURS BETWEEN THE DRAWING AND THE SITE BEFORE STARTING THE WORK

DRAWN: POTLURI CHINMAYI

ROLL NO: 22WU0301110


PROGRAM: INTERIOR DESIGN
SEM-V

DATE: 20-08-2024


SCALE: N.T.S.

SHEET TITLE: PLUMBING PLAN

PROJECT TITLE: G+3 VILLA

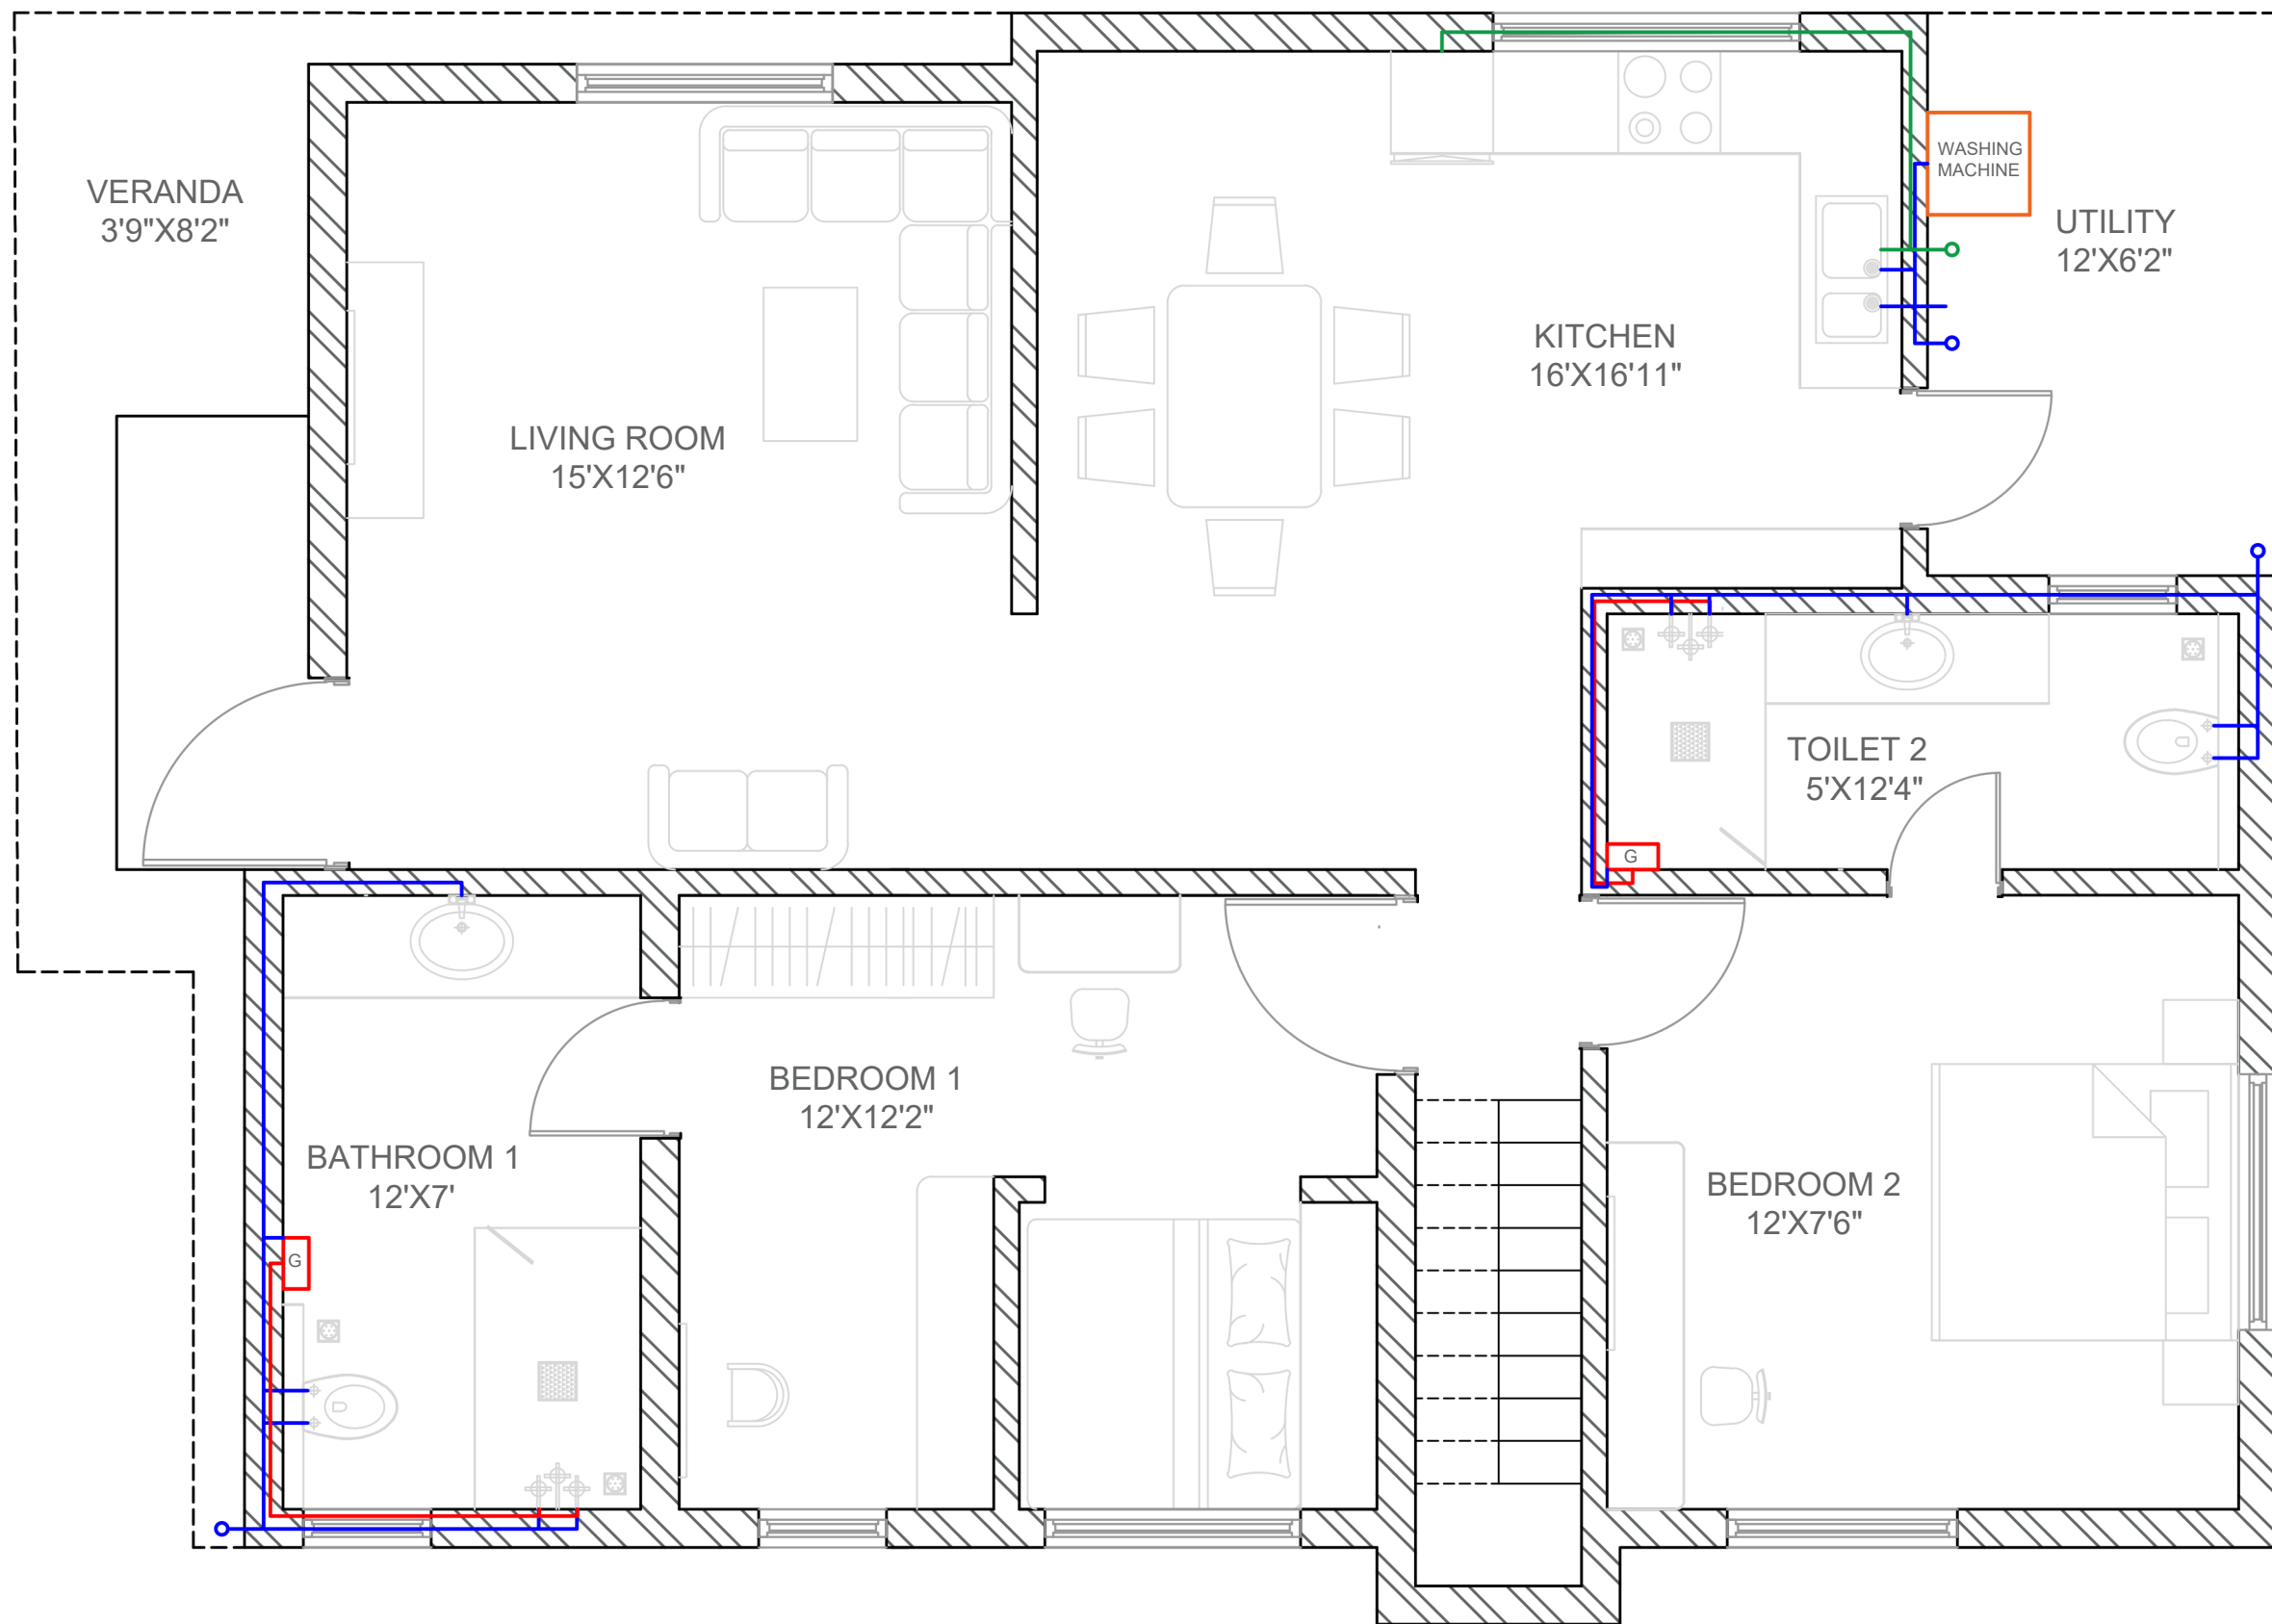

SIGNATURE

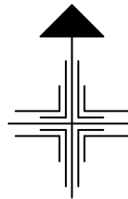

NOTES:

- 1. DIMENSIONS TO BE CHECKED AS PER SITE CONDITION.
- 2. ALL DIMENSIONS ARE IN FT AND INCHES UNLESS MENTIONED
- 3. DRAWINGS ARE TO BE READ AND NOT TO BE SCALED
- 4. ARCHITECT MUST BE NOTIFIED IF ANY DISCREPANCY OCCURS BETWEEN THE DRAWING AND THE SITE BEFORE STARTING THE WORK

DRAWN: POTLURI CHINMAYI

ROLL NO: 22WU0301110


PROGRAM: INTERIOR DESIGN SEM-V

DATE: 20-08-2024


SCALE: N.T.S.

SHEET TITLE: SANITARY LAYOUT

PROJECT TITLE: G+3 VILLA

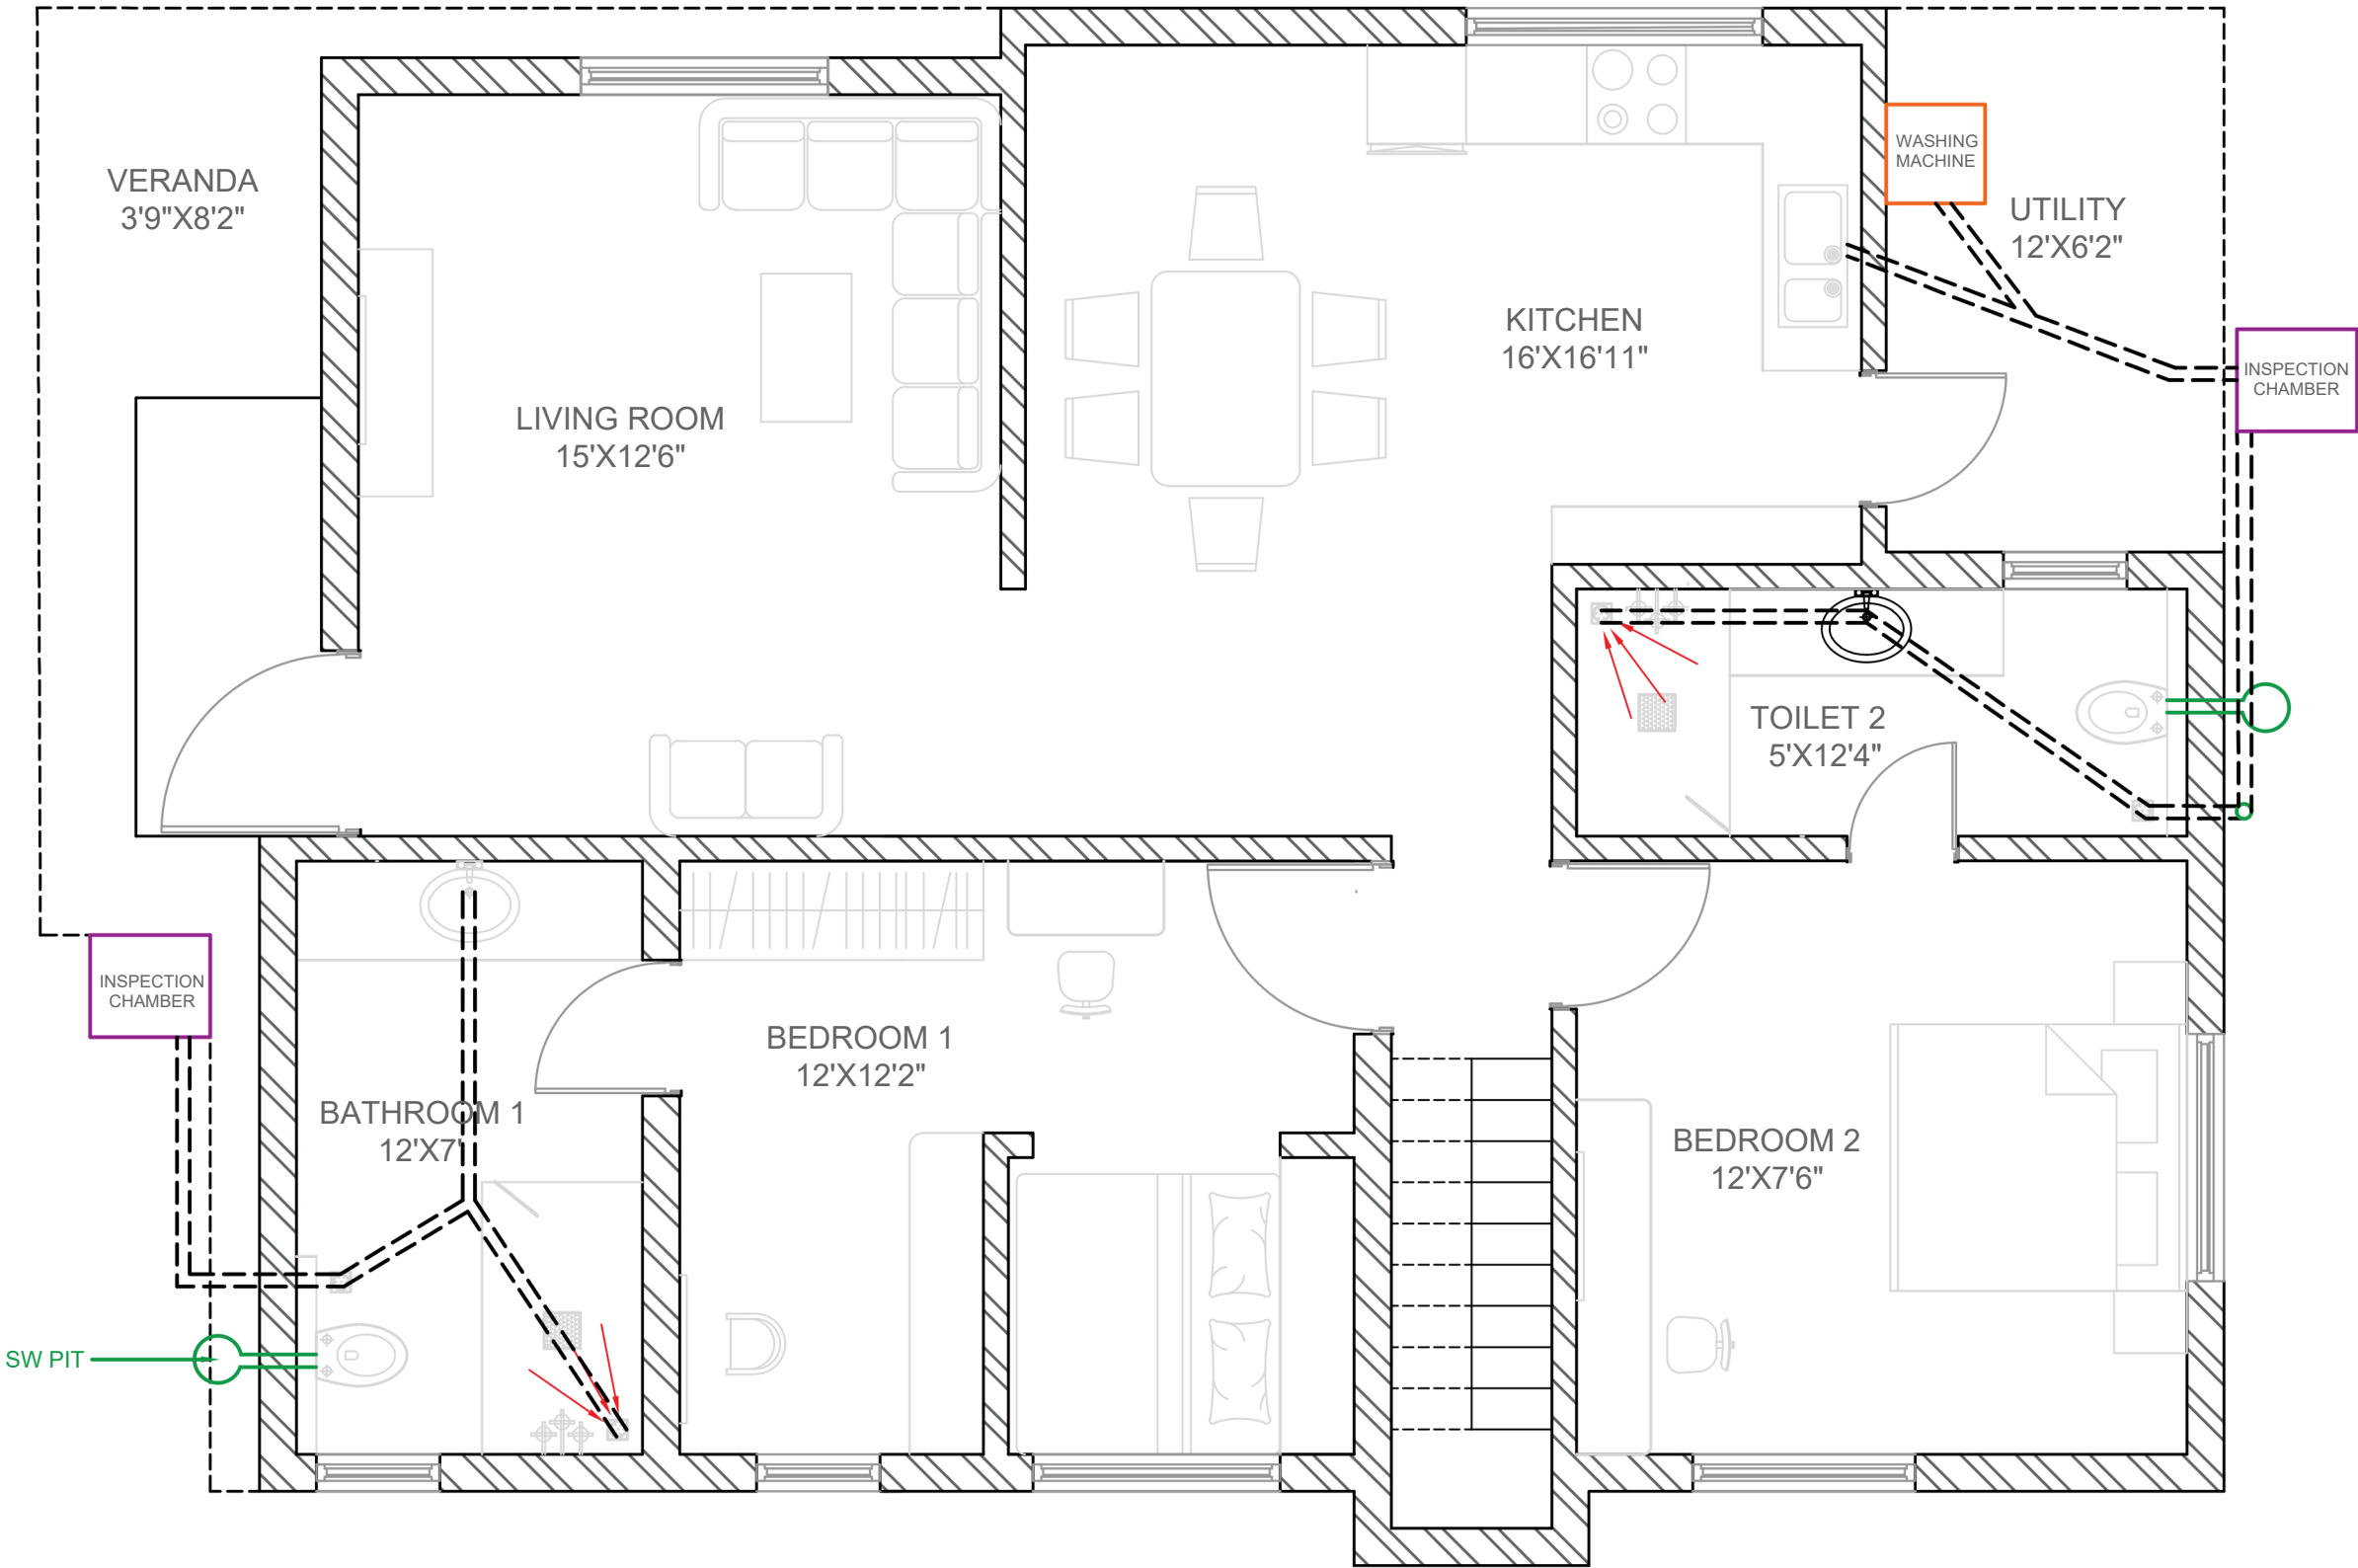


SIGNATURE

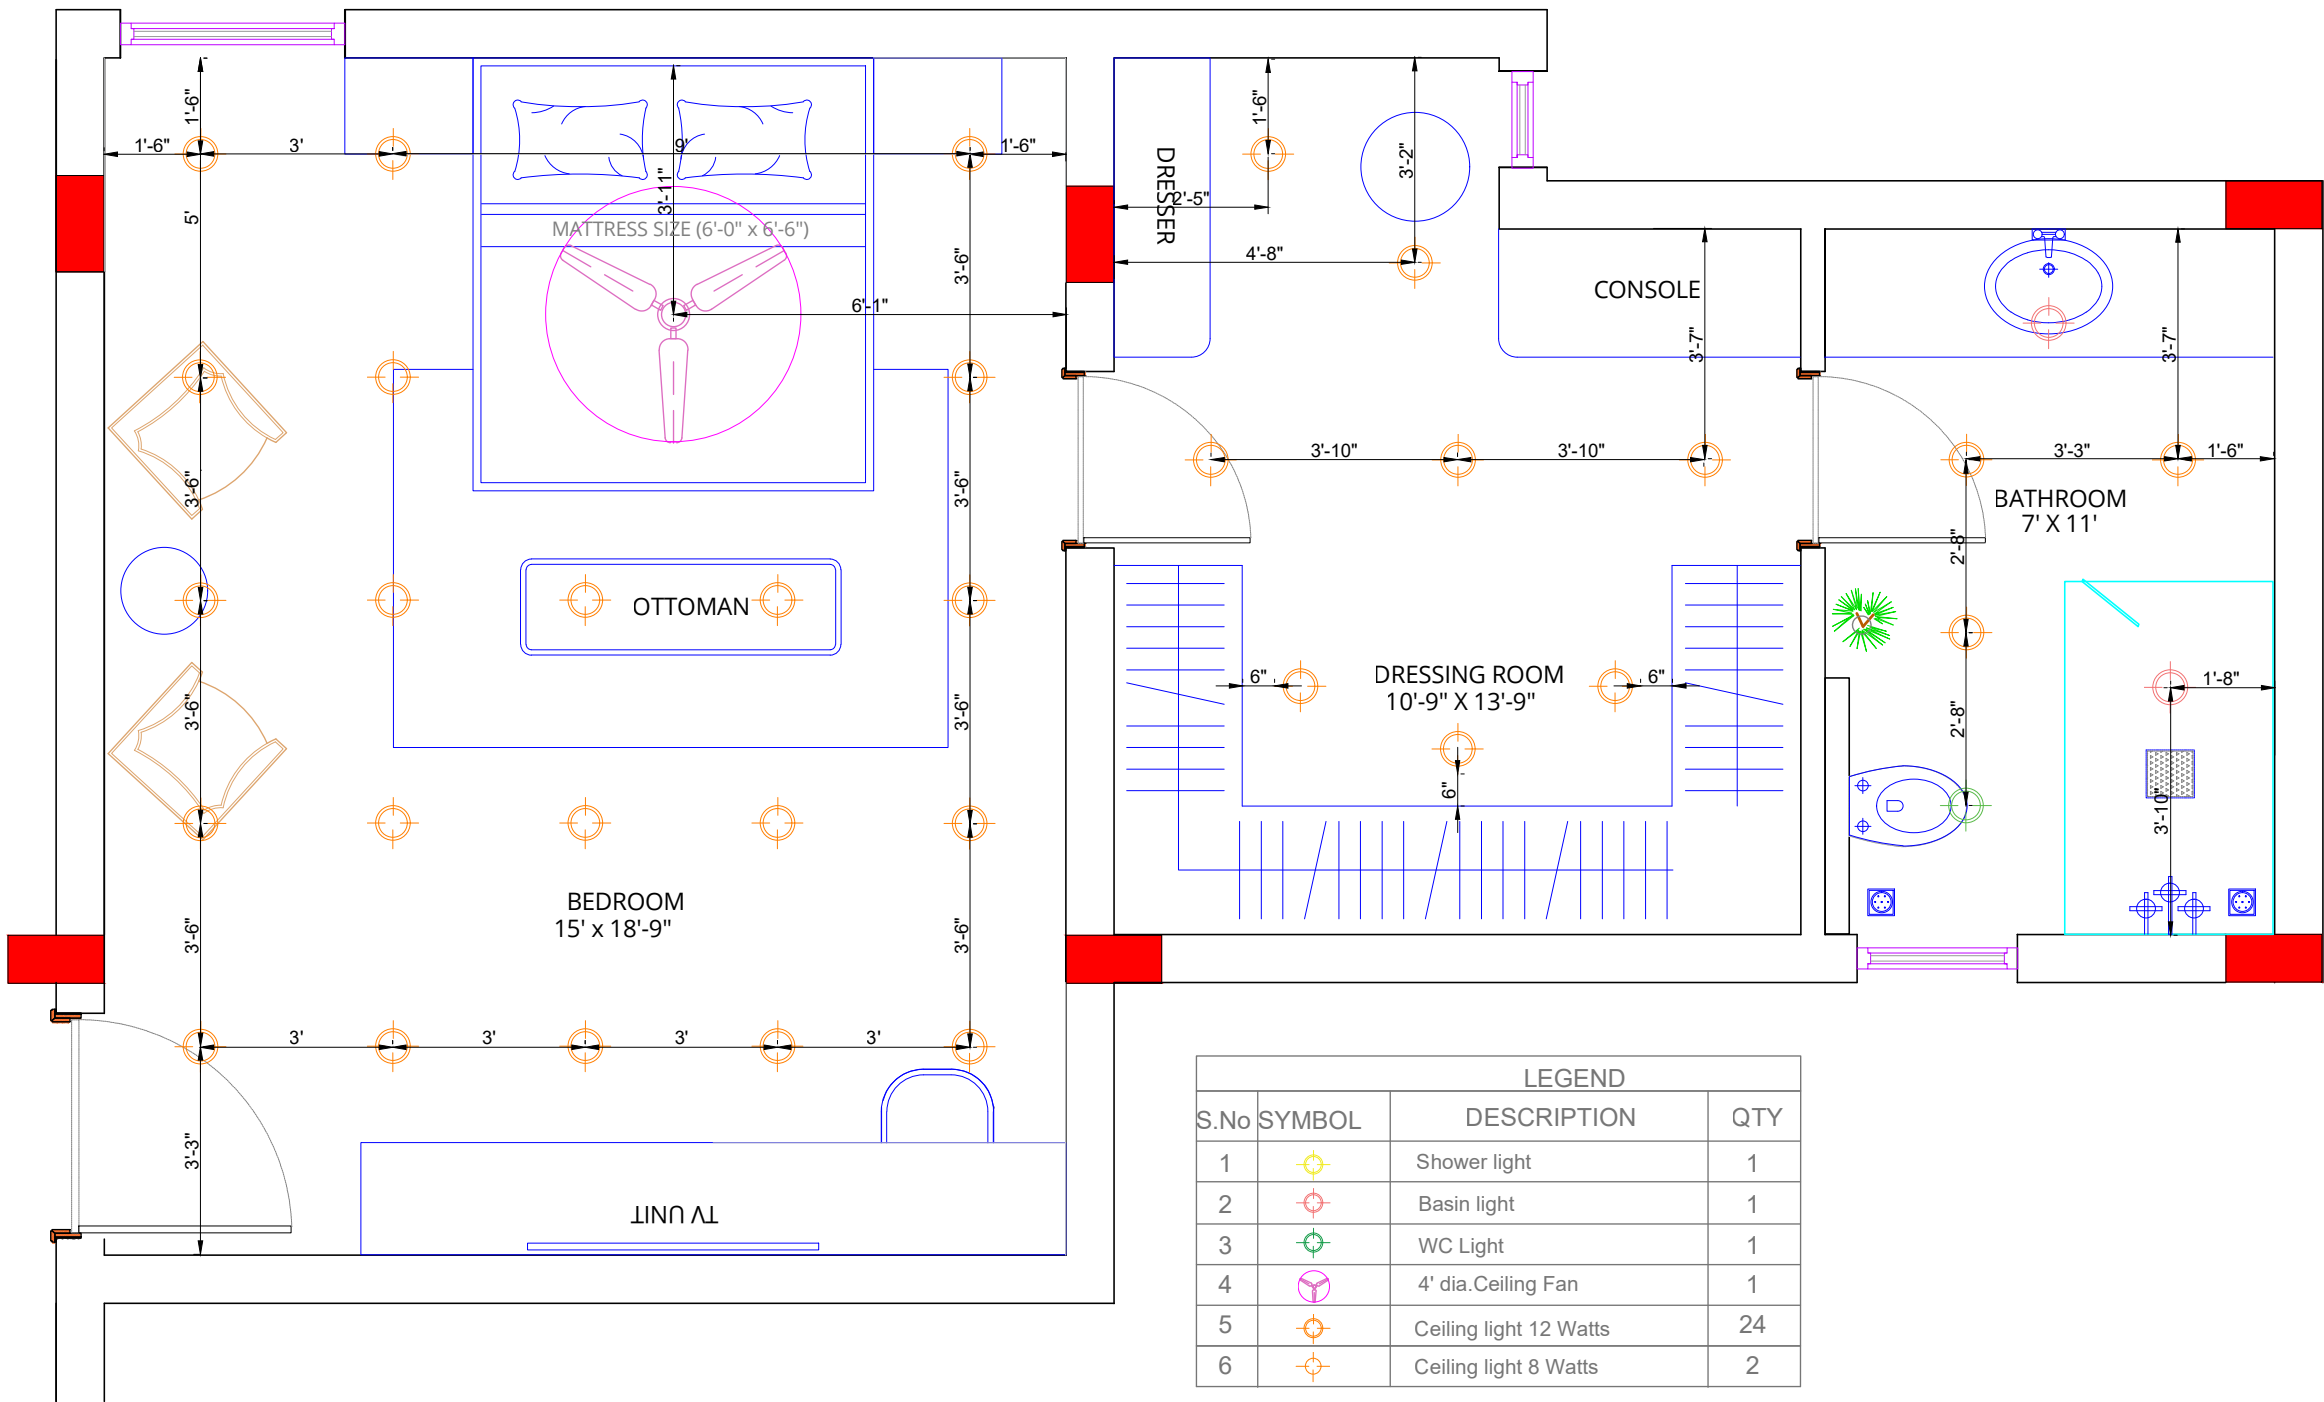

OLIVE HOUSE INTERIOR STUDIO
HAS THE COPY RIGHTS OF THIS DOCUMENT, AND IT SHOULDN'T BE USED BY ANYBODY WITHOUT THEIR PERMISSION ***

GENERAL NOTE
1. All dimensions are in feet and inches unless specified.
2. don't scale this drawing, only written dimensions are to be followed

SIGNATURE	DIRECTION 	CLIENT :-Mr. ROHIT
		PROJECT :-PROPOSED BEDROOM INTERIORS @ RAICHUR
TITLE :-ELECTRICAL LAYOUT		

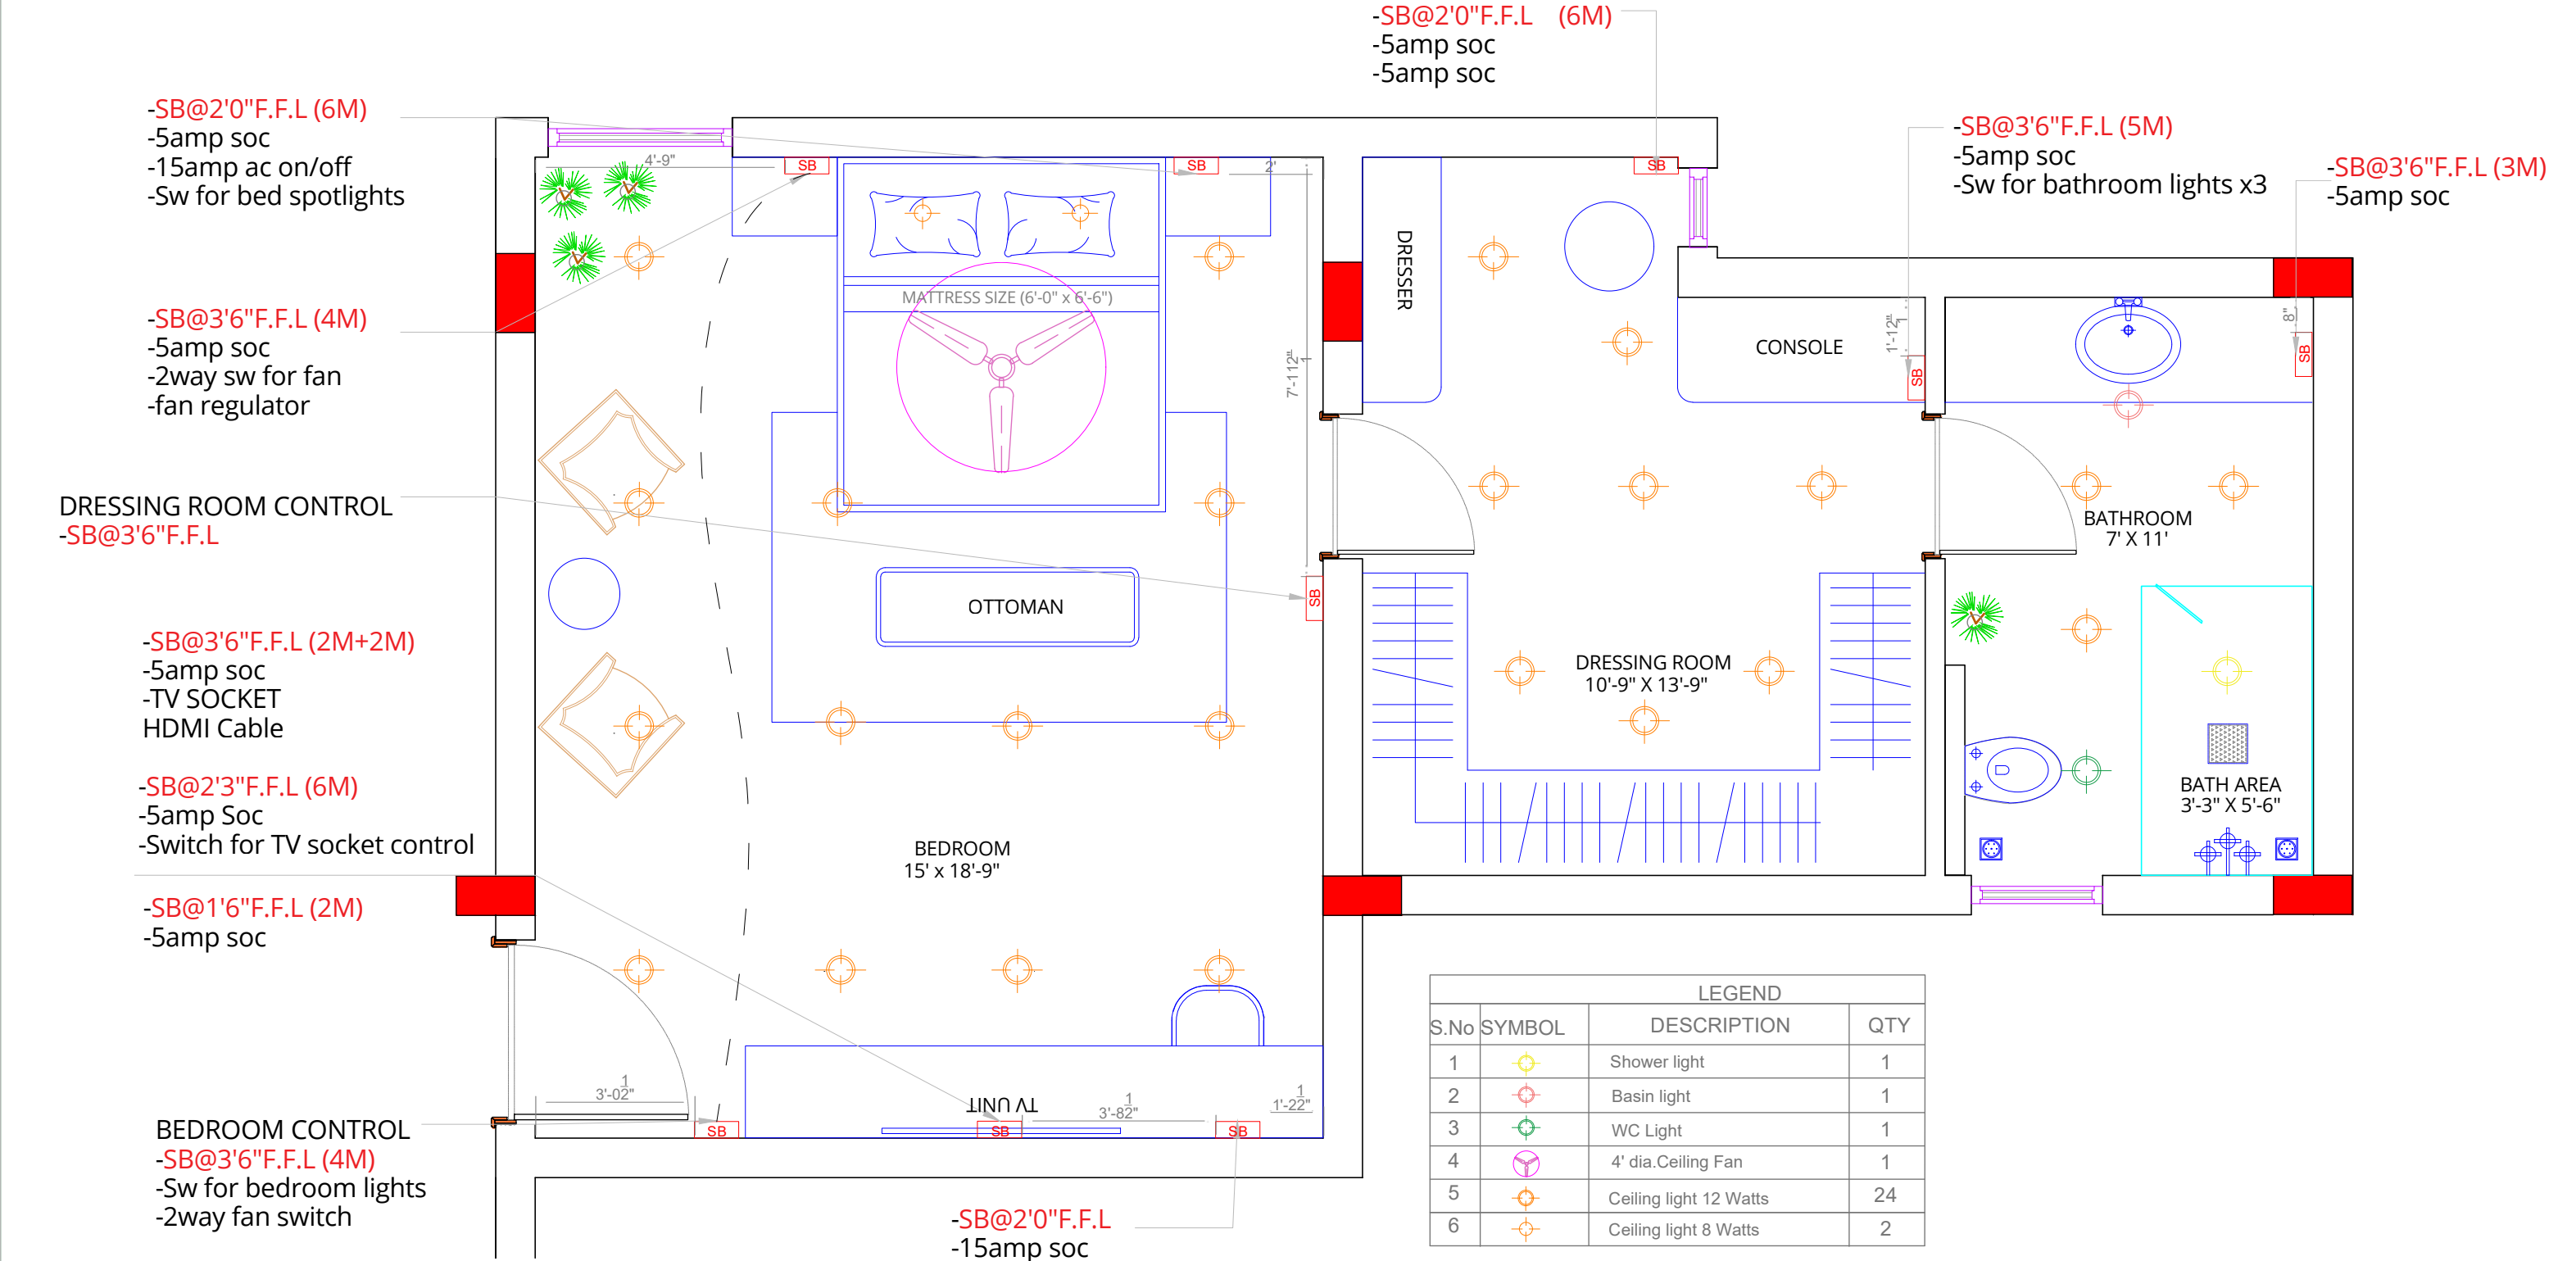

OLIVE HOUSE INTERIOR STUDIO

HAS THE COPY RIGHTS OF THIS DOCUMENT, AND IT SHOULDN'T BE USED BY ANYBODY WITHOUT THEIR PERMISSION ***

GENERAL NOTE

1. All dimensions are in feet and inches unless specified.
2. don't scale this drawing, only written dimensions are to be followed

SIGNATURE

TITLE :-ELECTRICAL LAYOUT


DIRECTION


E


N S

CLIENT :-Mr. ROHIT

PROJECT :-PROPOSED BEDROOM INTERIORS @ RAICHUR

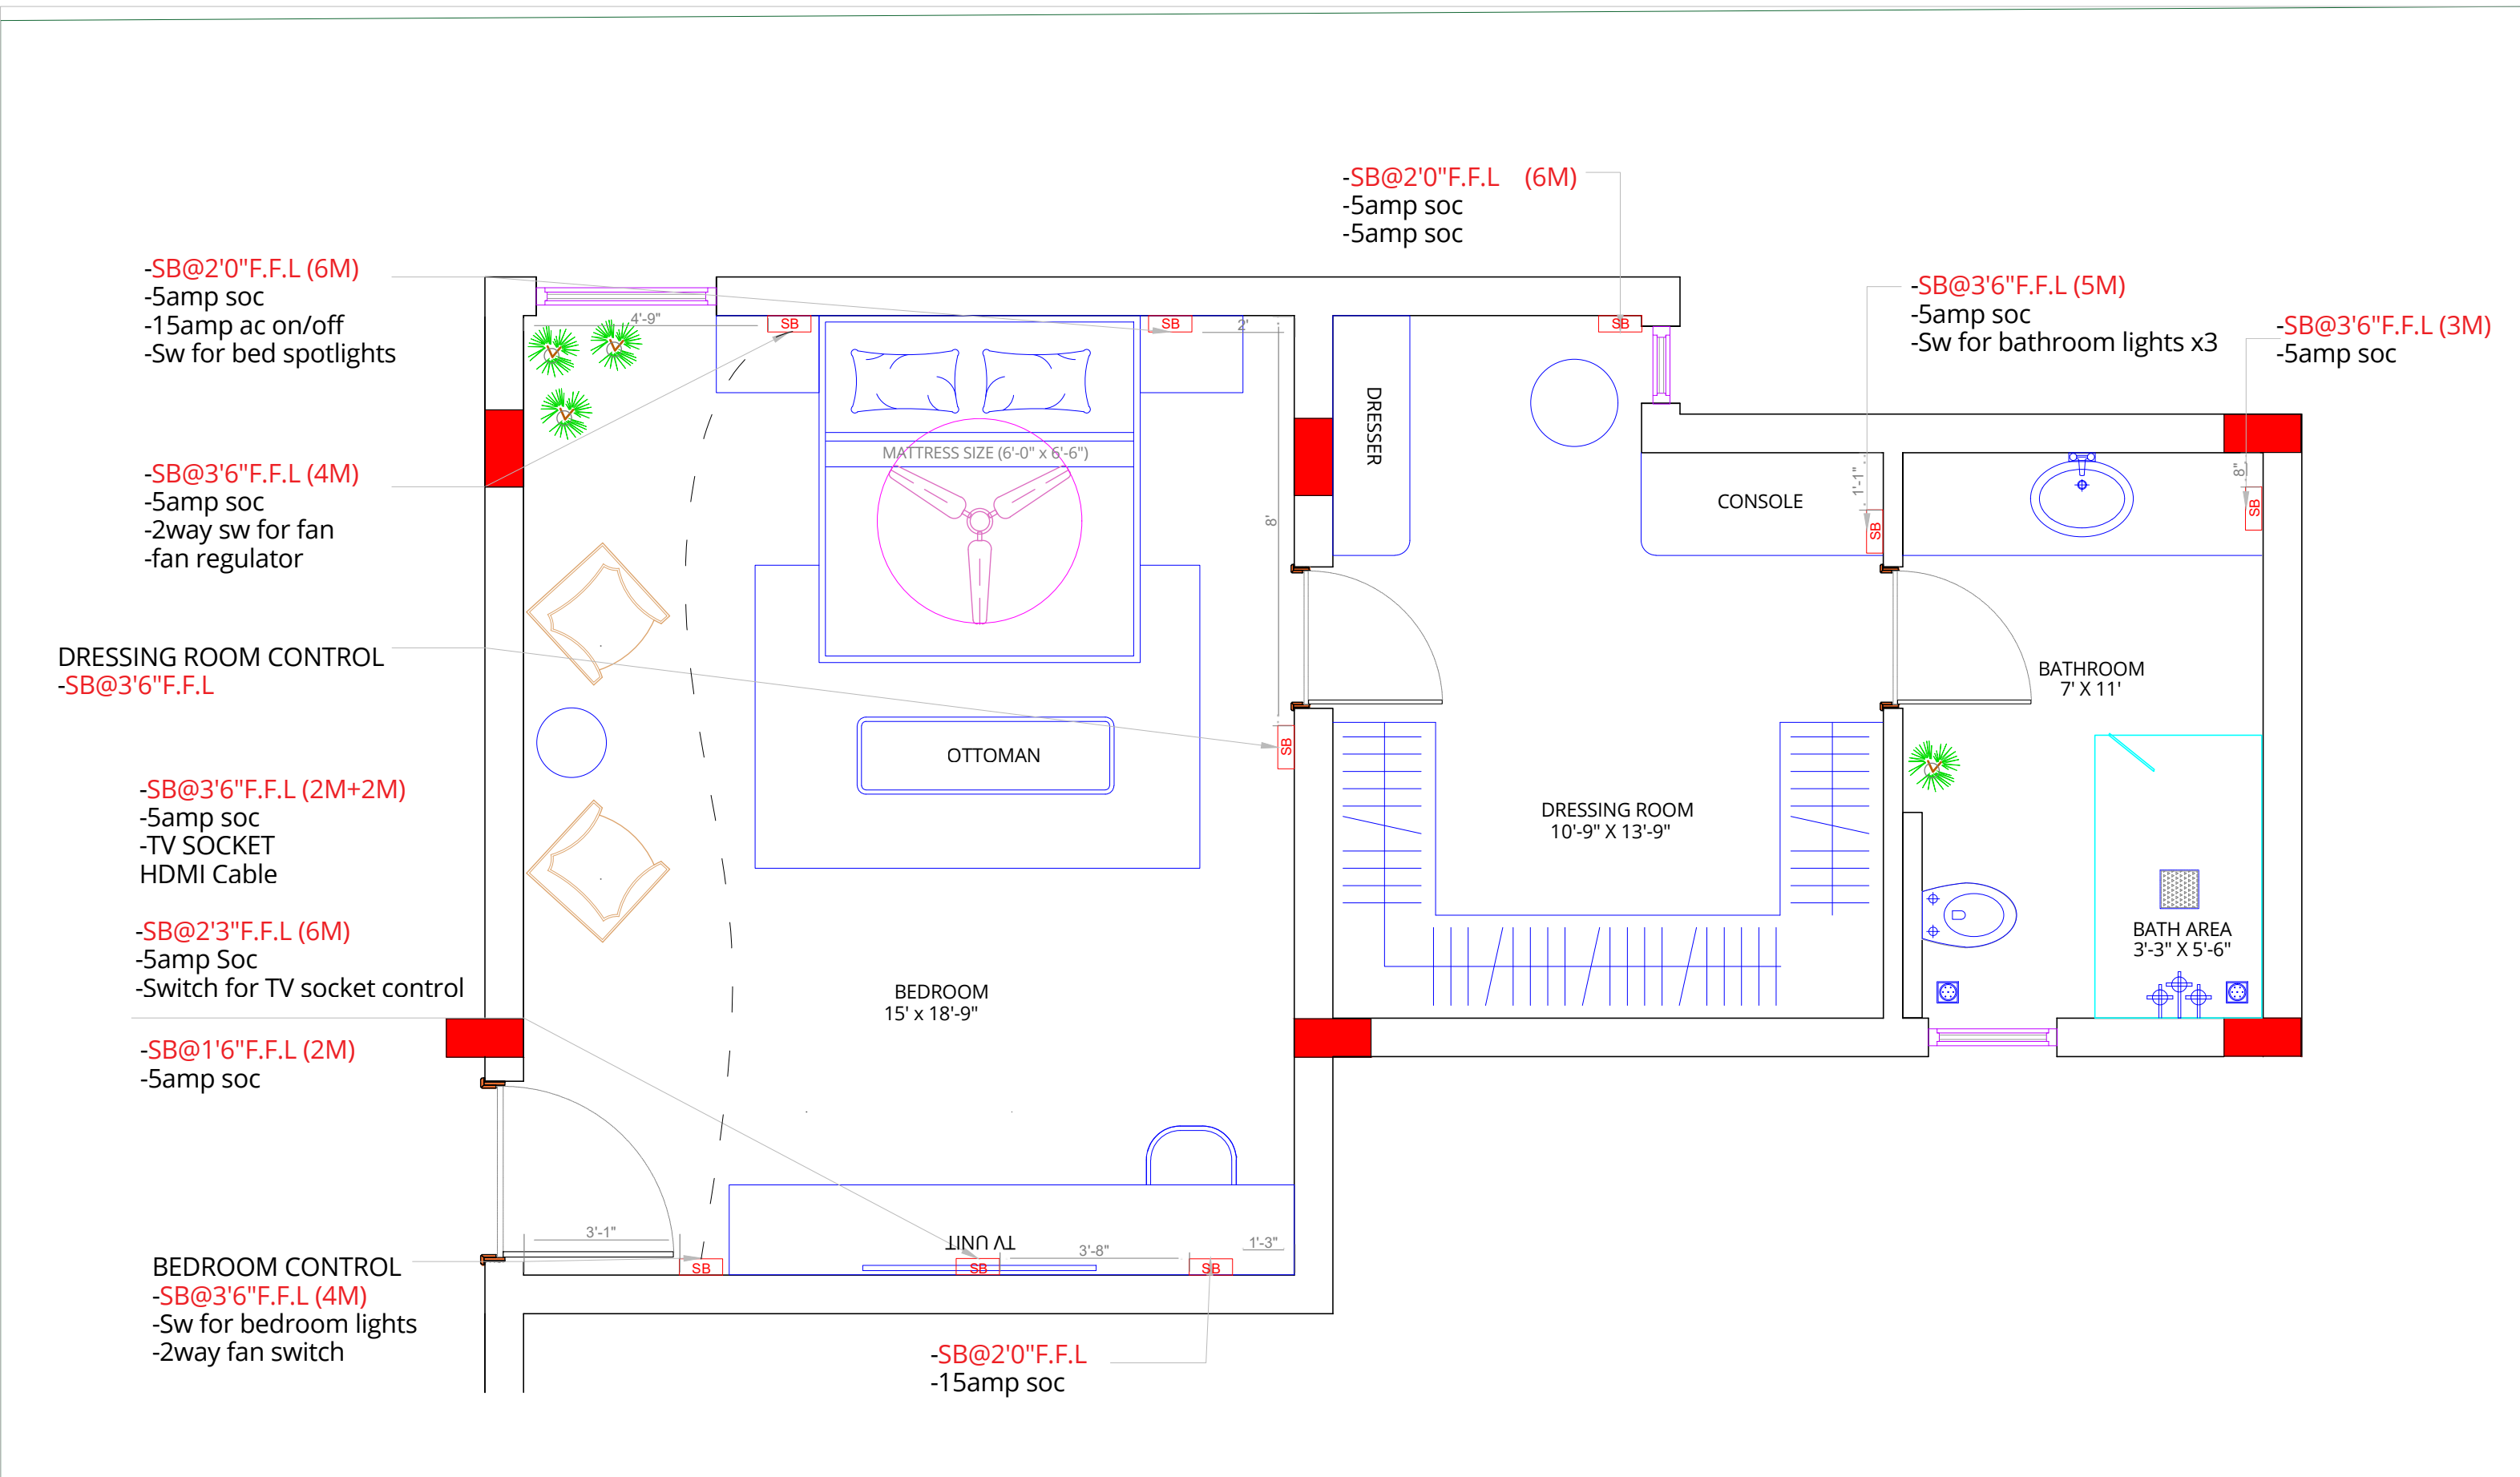

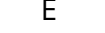OLIVE HOUSE INTERIOR STUDIO HAS THE COPY RIGHTS OF THIS DOCUMENT, AND IT SHOULDN'T BE USED BY ANYBODY WITHOUT THEIR PERMISSION ***	SIGNATURE TITLE :-ELECTRICAL LAYOUT	DIRECTION	CLIENT :-Mr. ROHIT	
		E N S W 	PROJECT :-PROPOSED BEDROOM INTERIORS @ RAICHUR	
GENERAL NOTE 1. All dimensions are in feet and inches unless specified. 2. don't scale this drawing, only written dimensions are to be followed				

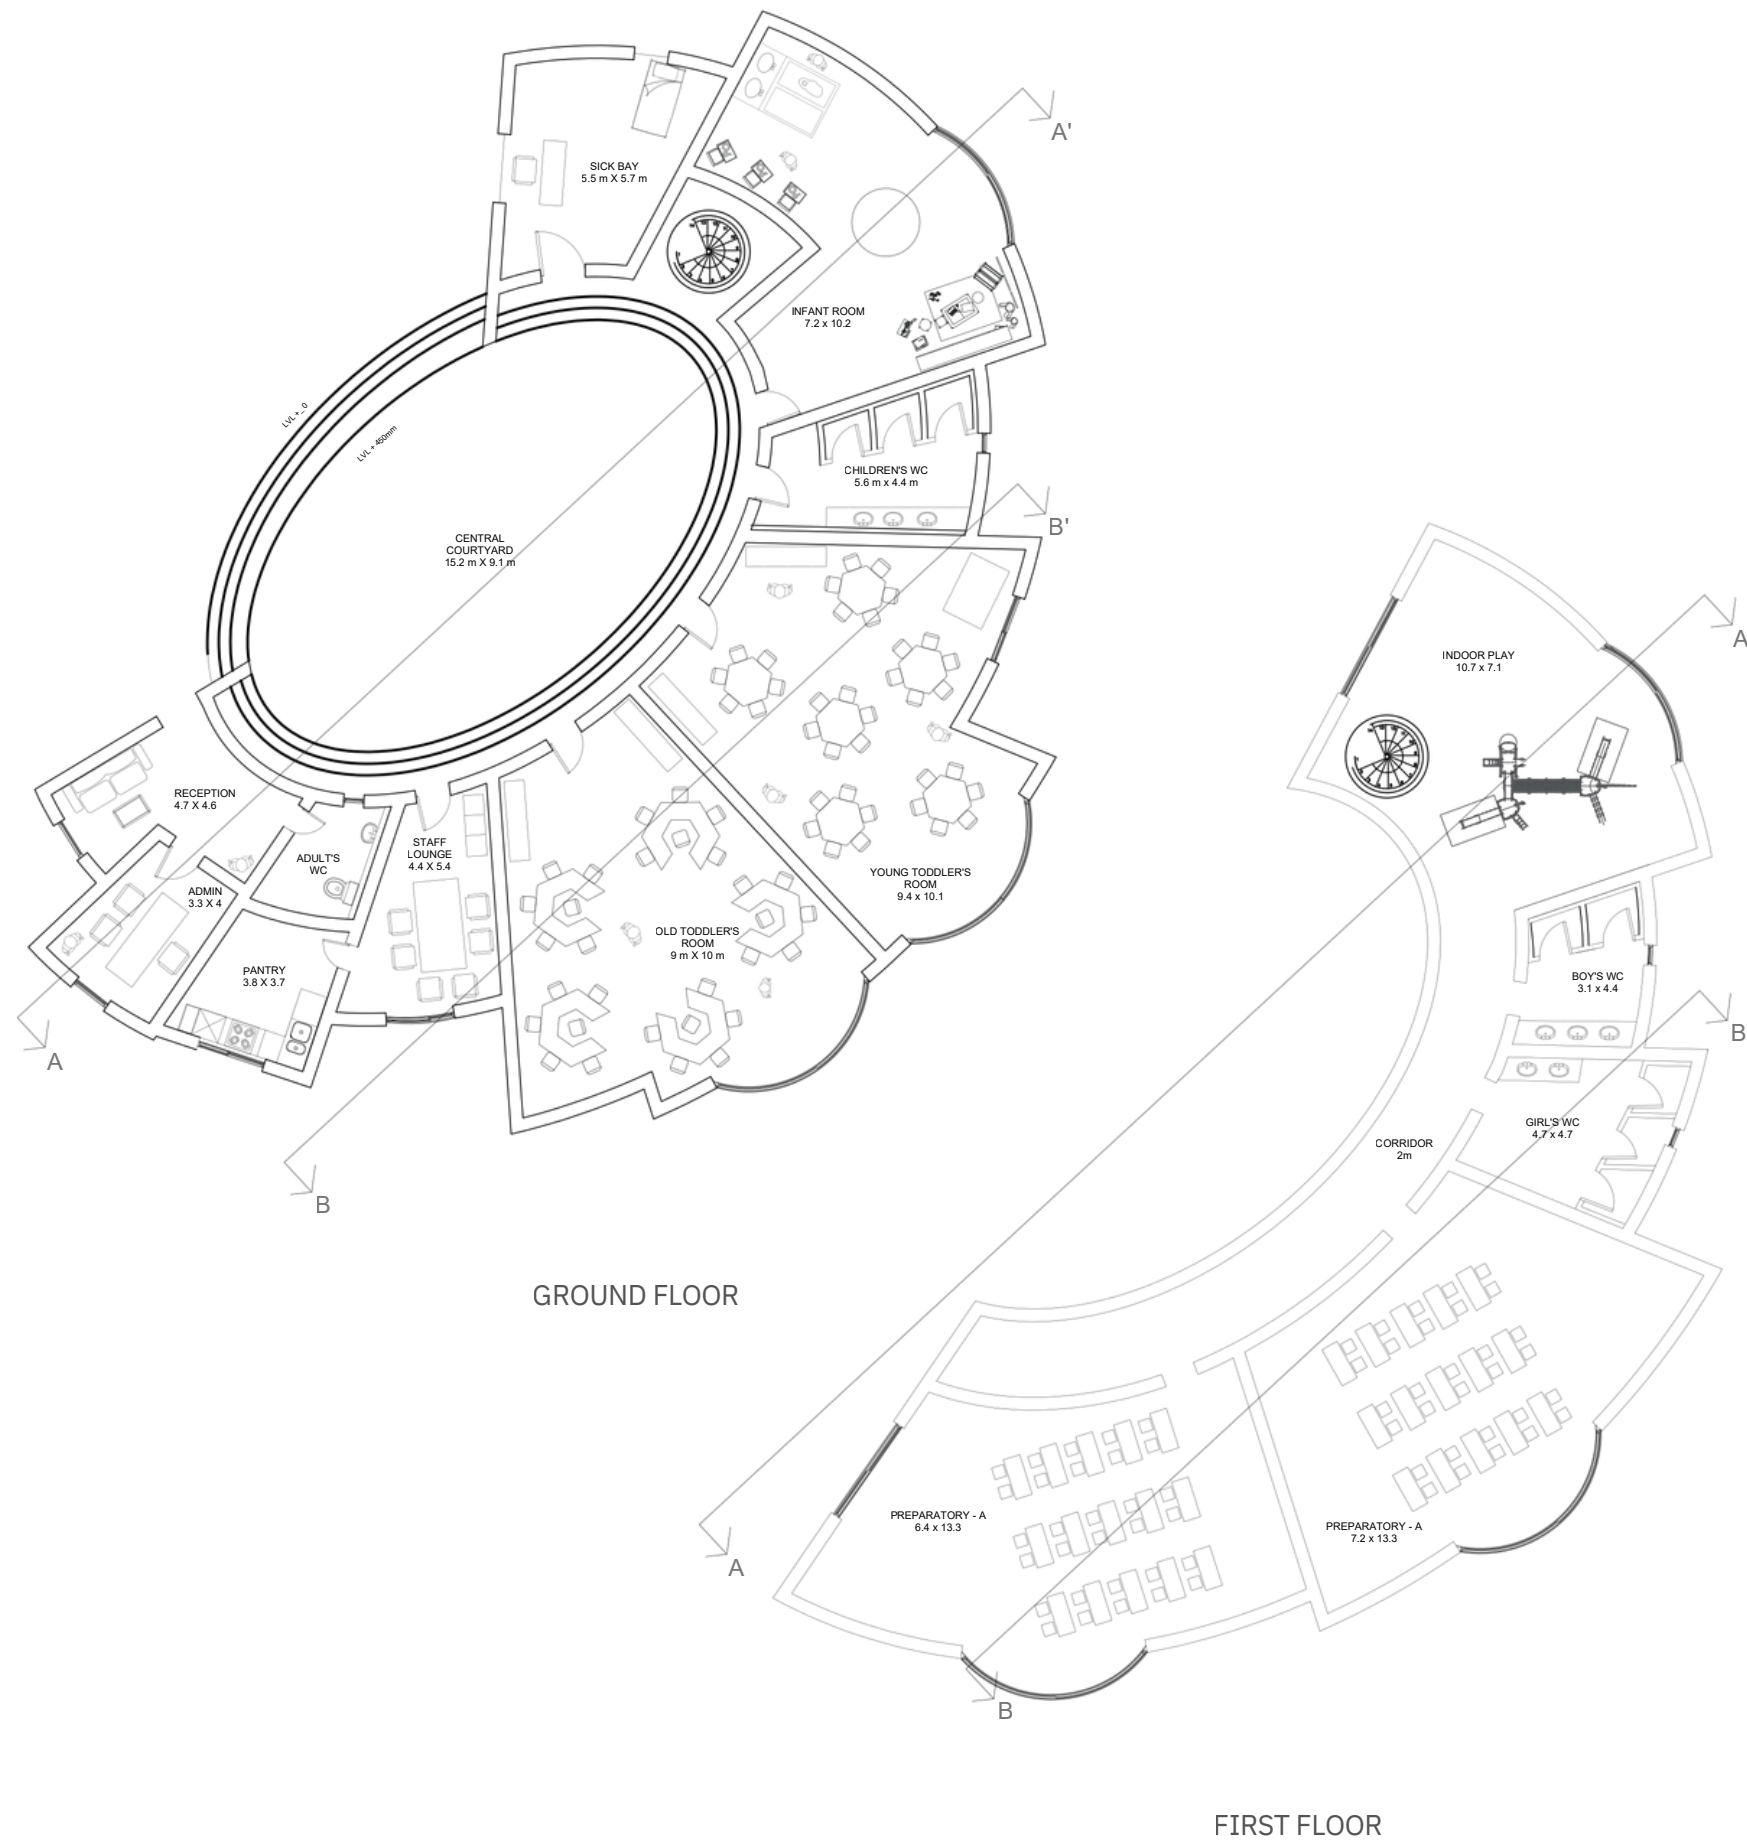

GROUND FLOOR

FIRST FLOOR


NOTE: ALL DIMENSIONS ARE IN MM

SCALE: PLAN - 1:100	NORTH: 
------------------------	---

NAME: POTLURI CHINMAYI
STUDENT ID: 22WU0301110
GUIDE : AR. TEJAS EKNATH PAWAR
INTERIOR DESIGN-SOAD, WOXSSEN UNIVERSITY



SHEET NO : 01/01	STAMP :
-------------------------	---------

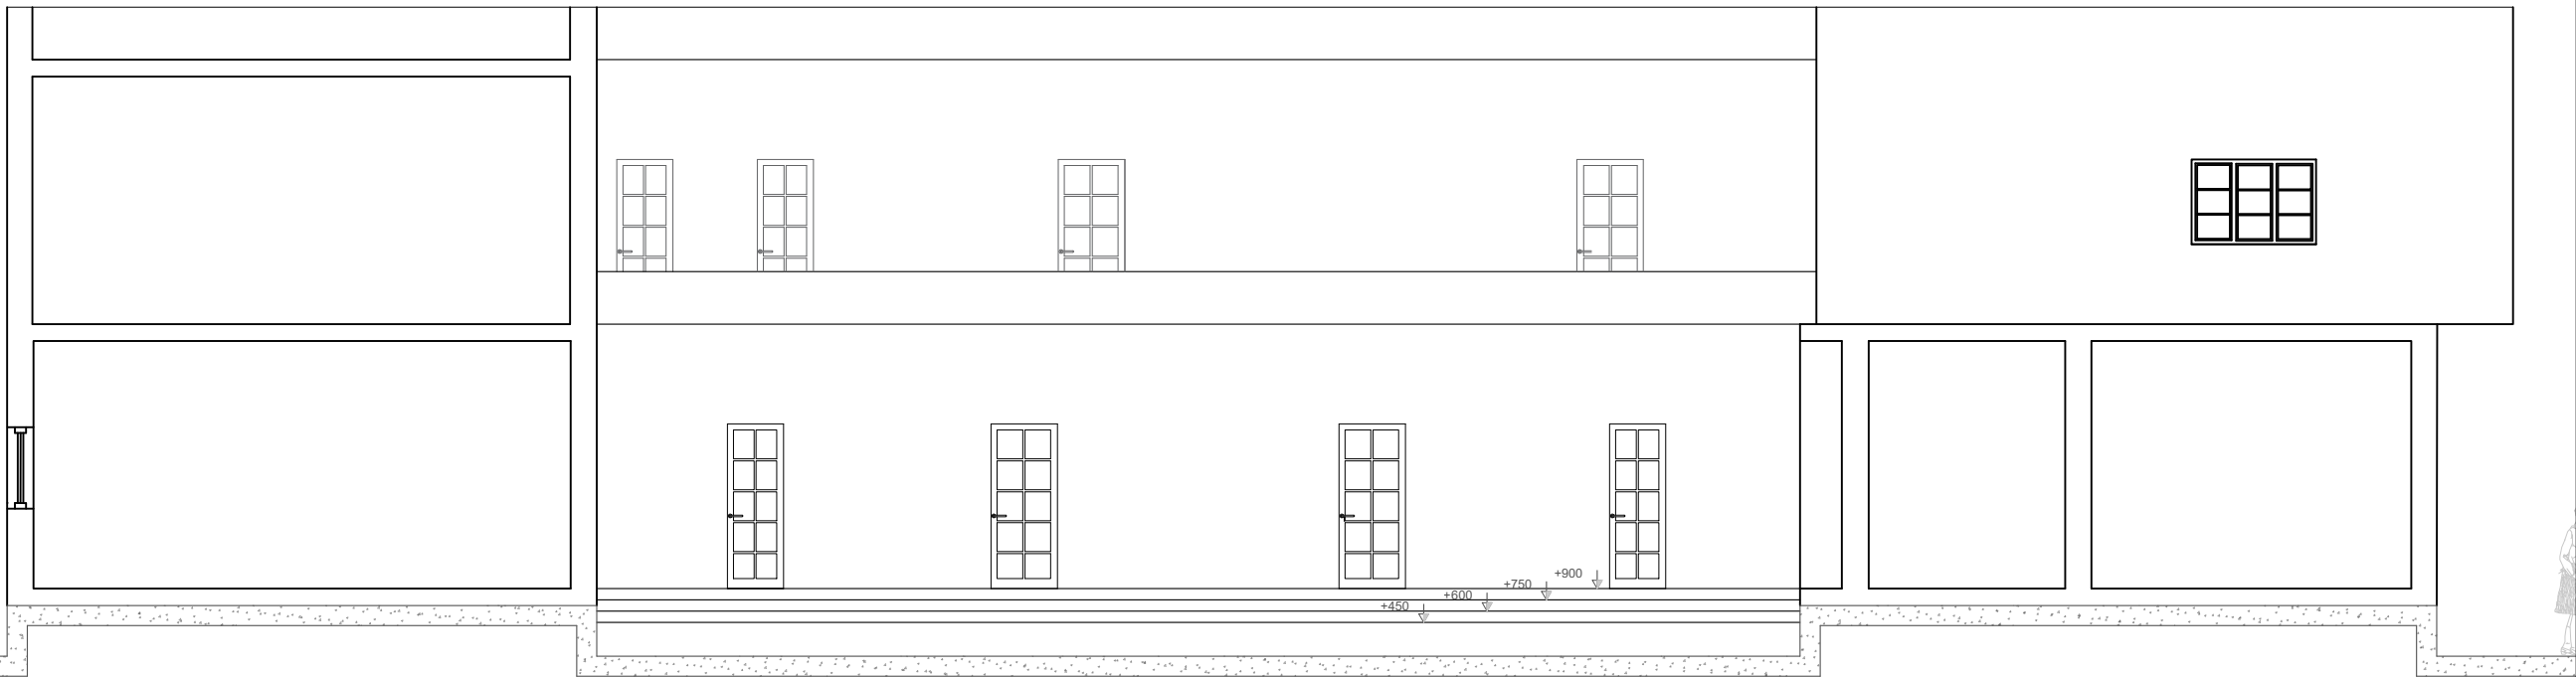

SECTION A-A'



SECTION B-B'

NOTE: ALL DIMENSIONS ARE IN MM

SCALE:

PLAN - 1:100

NORTH:



NAME: POTLURI CHINMAYI

STUDENT ID: 22WU0301110

GUIDE : AR. TEJAS EKNATH PAWAR

INTERIOR DESIGN-SOAD, WOXSSEN UNIVERSITY



SHEET NO :

01/01

STAMP :

PROJECT TITLE : THE CATALYST, PRE-SCHOOL DESIGN